


ΔΡΟΜΟΣ

A

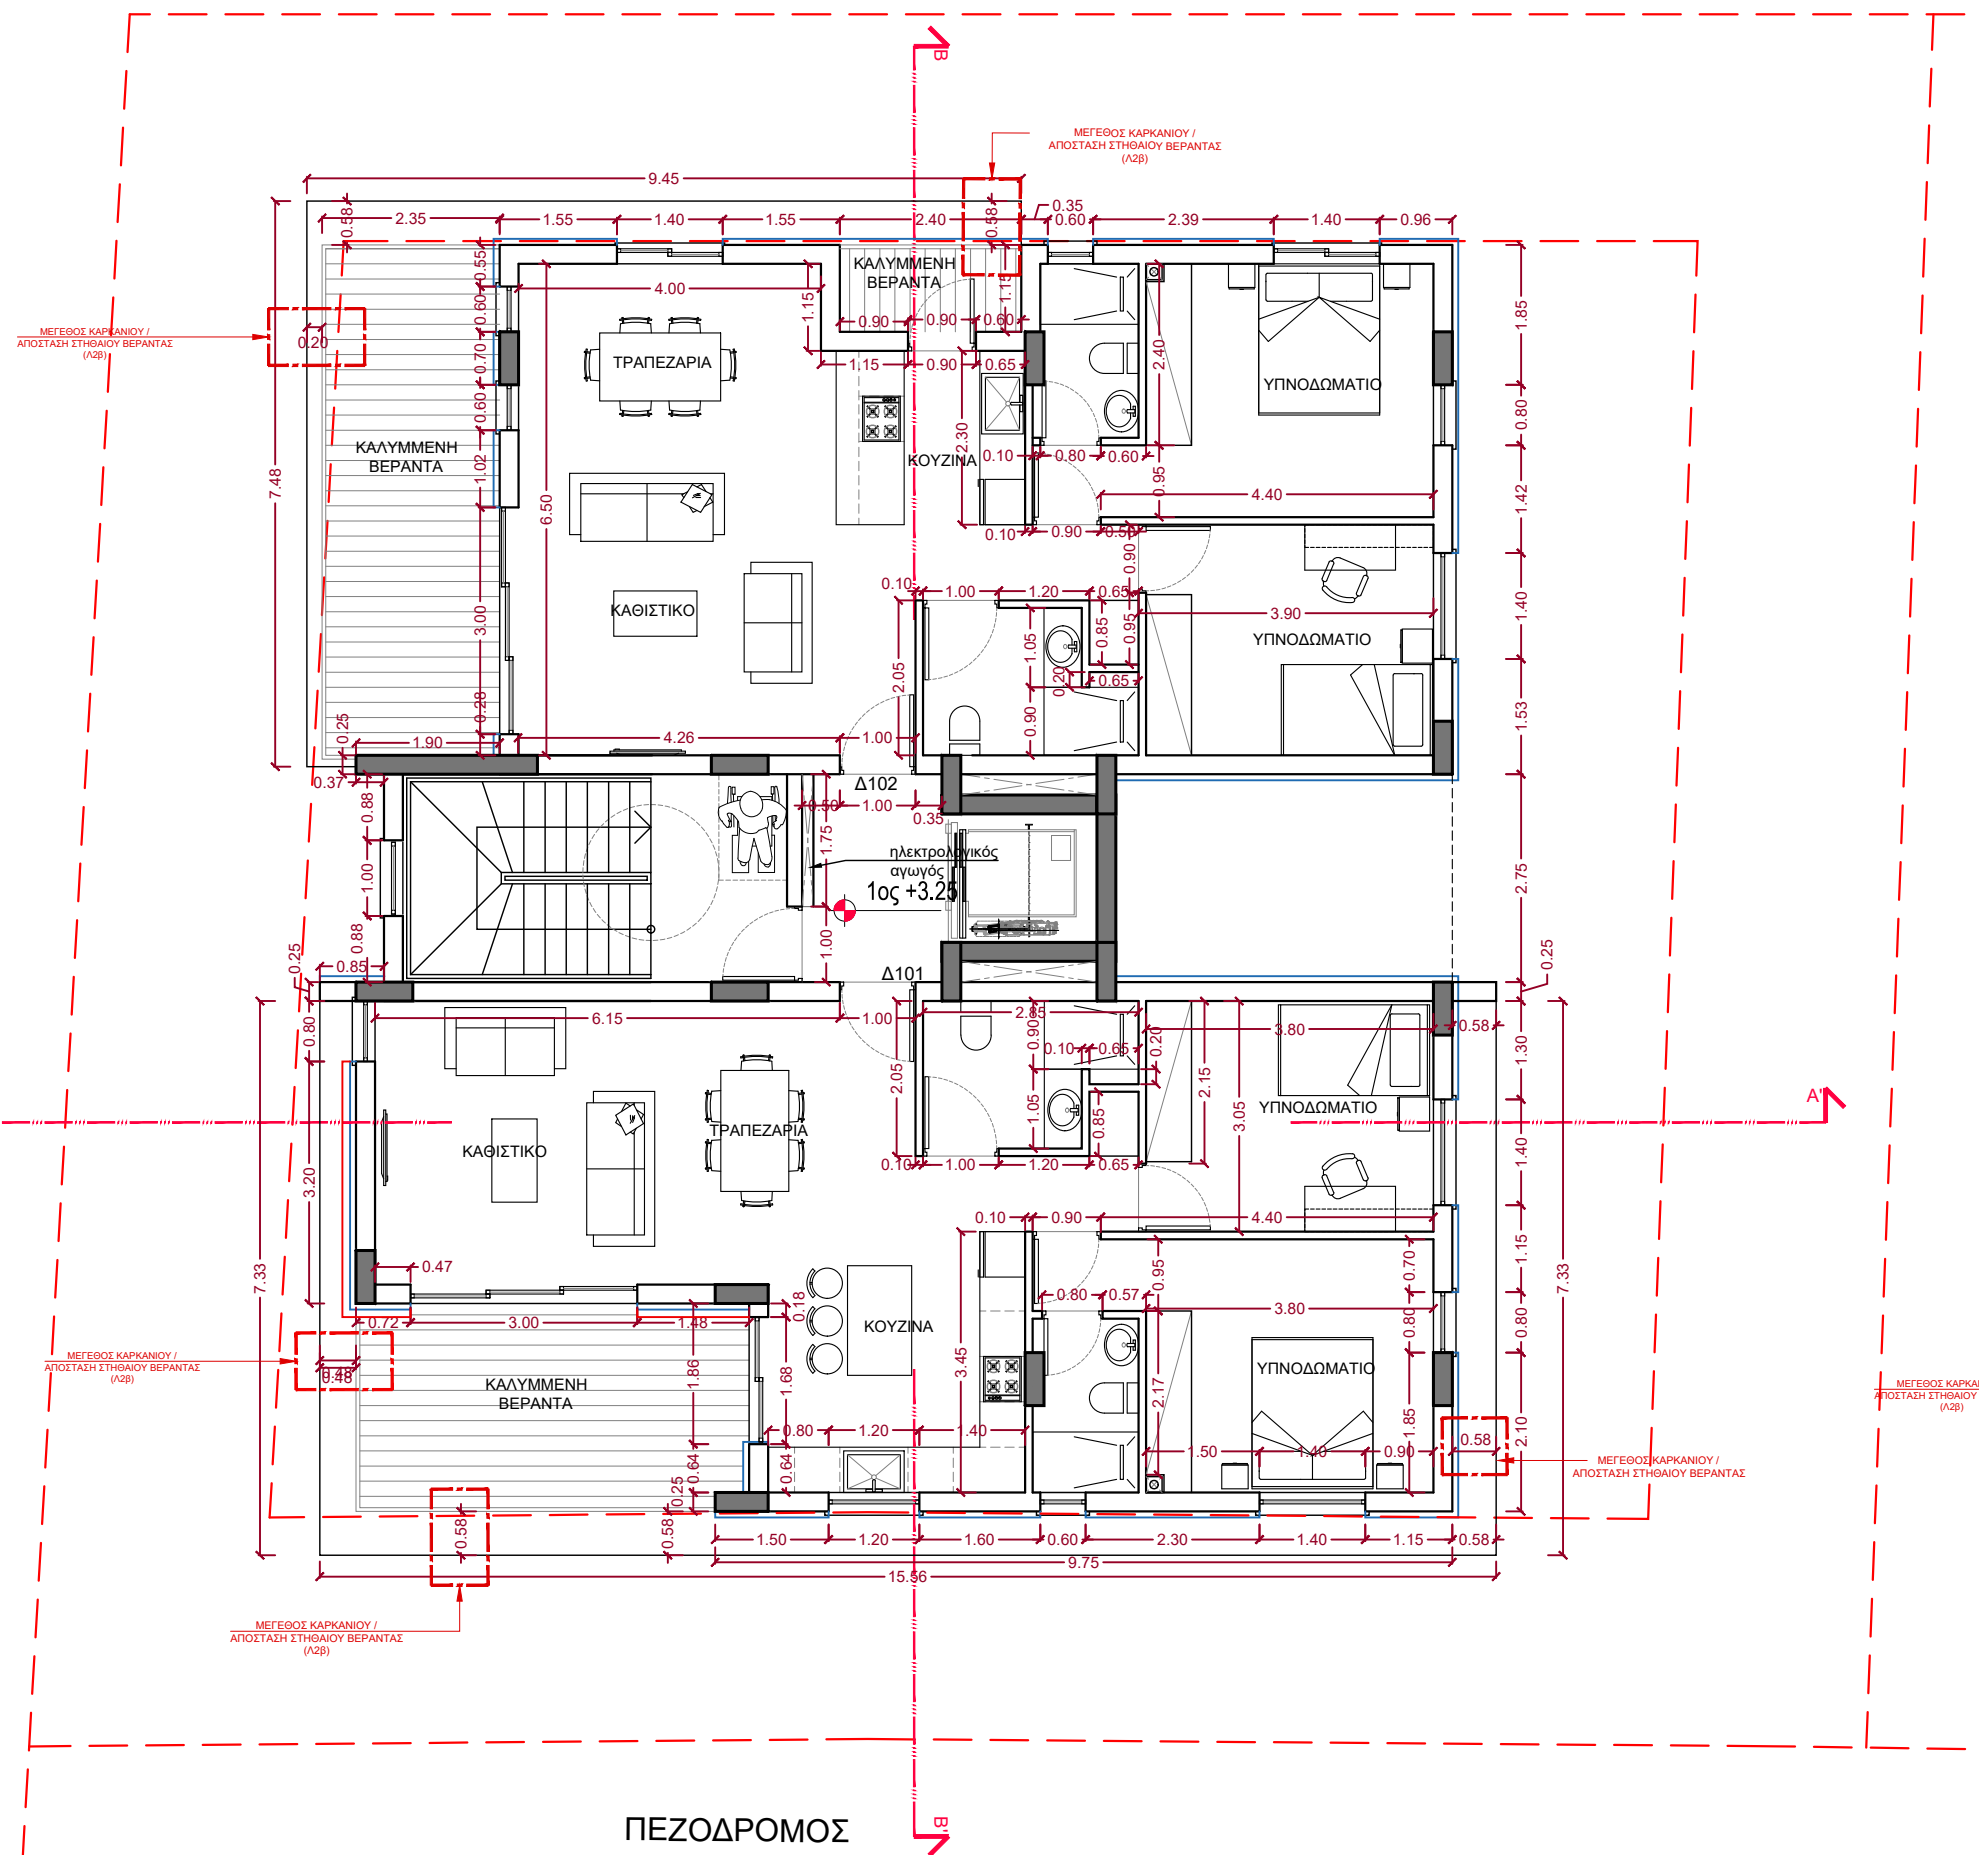

ΠΕΖΟΔΡΟΜΟΣ

B

ΚΑΤΟΨΗ 1ου ΟΡΟΦΟΥ DUE



ARKIDEA ARCHITECTS

Marios Georgiou
Architect
BA(Hons) DipArch
Reg. Number 86602

4th, Andrea Assioti Street
2007, Strovolos, Nicosia, Cyprus
Tel : +357-99-665412
email : marios@arkideaarchitects.com

NOTES / REVISIONS

PROJECT NAME

Magnum Opus Due

DRAWING TITLE

ΚΑΤΟΨΗ 1ου

DATE

27/01/26

SCALE


1:100

JOB NUMBER

TEMAXIO 1172


DRAWING No.

A01

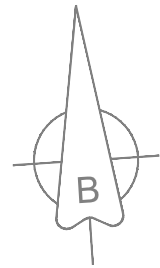

ΔΡΟΜΟΣ

A

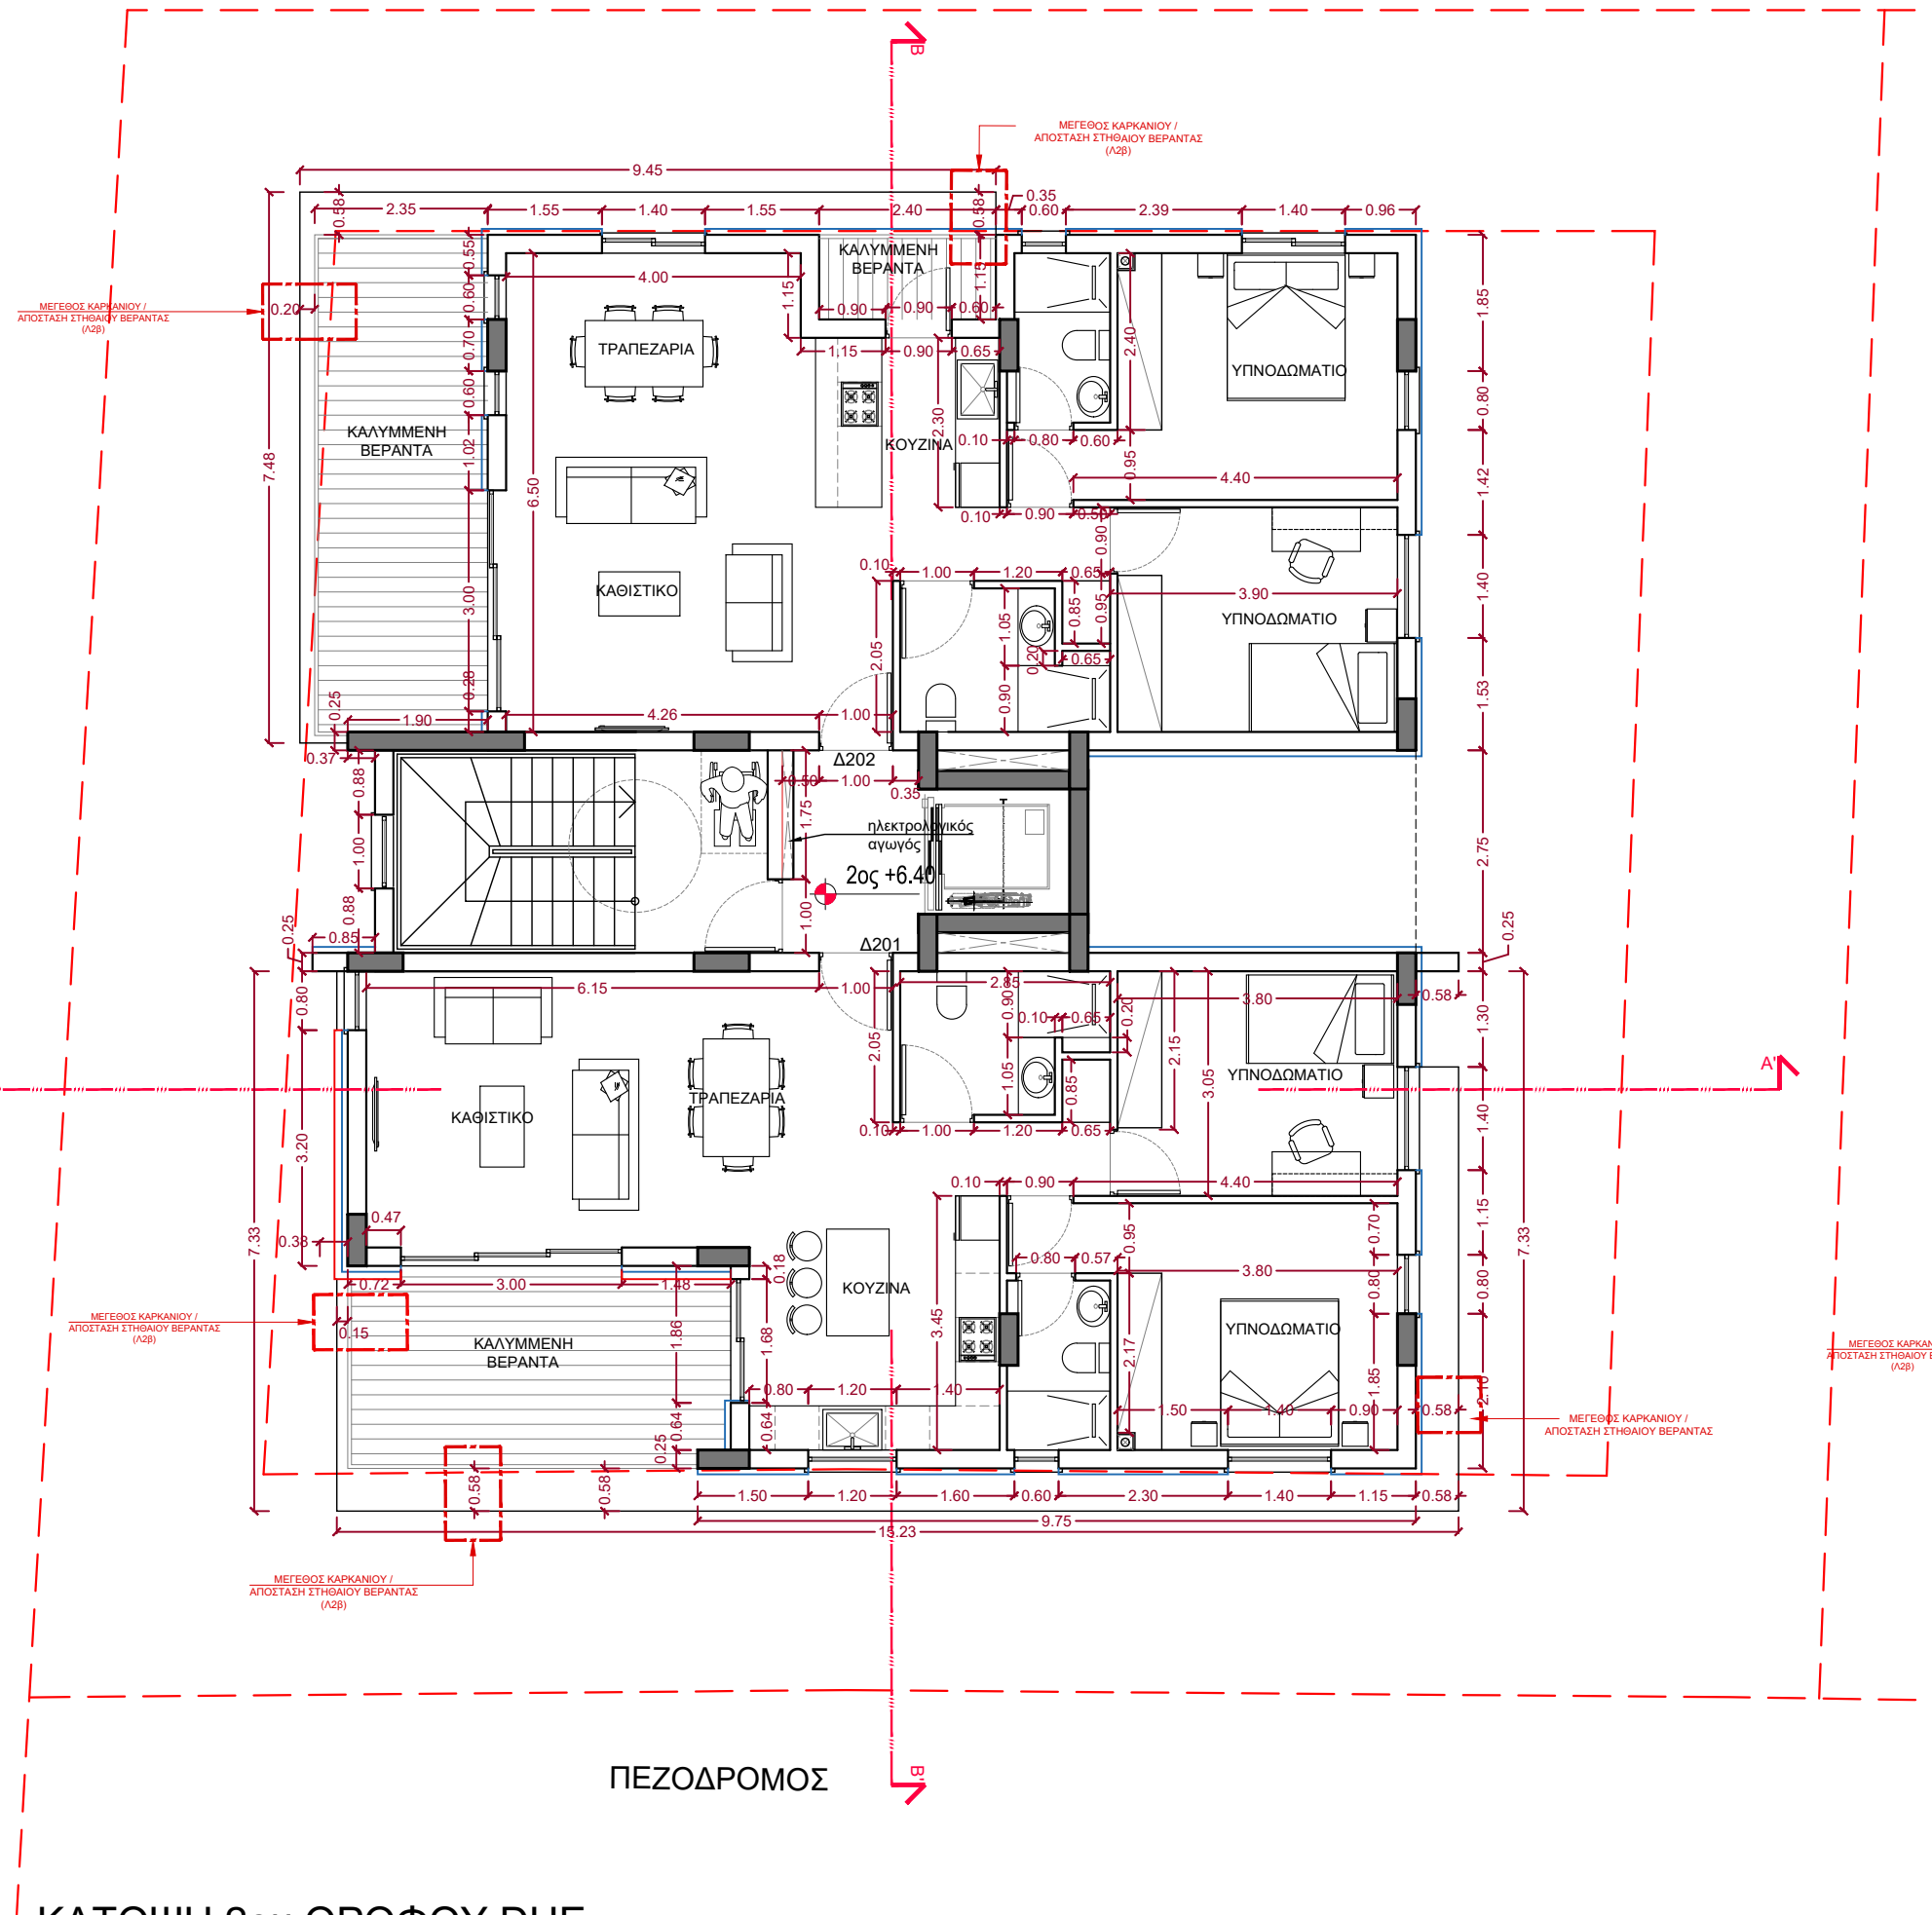

ARKIDEA ARCHITECTS

Marios Georgiou
Architect
BA(Hons) DipArch
Reg. Number 86602

4th, Andrea Assioti Street
2007, Strovolos, Nicosia, Cyprus
Tel : +357-99-665412
email : marios@arkideaarchitects.com

NOTES / REVISIONS

PROJECT NAME

Magnum Opus Due

DRAWING TITLE

ΚΑΤΟΨΗ 2ου


DATE	SCALE
27/01/26	1:100
JOB NUMBER	DRAWING No.
TEMAXIO 1172	A02



4^A, Andrea Assioli Street
2007, Strovolos, Nicosia, Cyprus
Tel : +357-99-665412
email : marios@arkideearchitects.com


NOTES / REVISIONS

TEMAXIO 1172	A03
--------------	-----

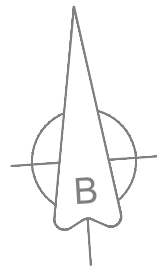

ΔΡΟΜΟΣ

A

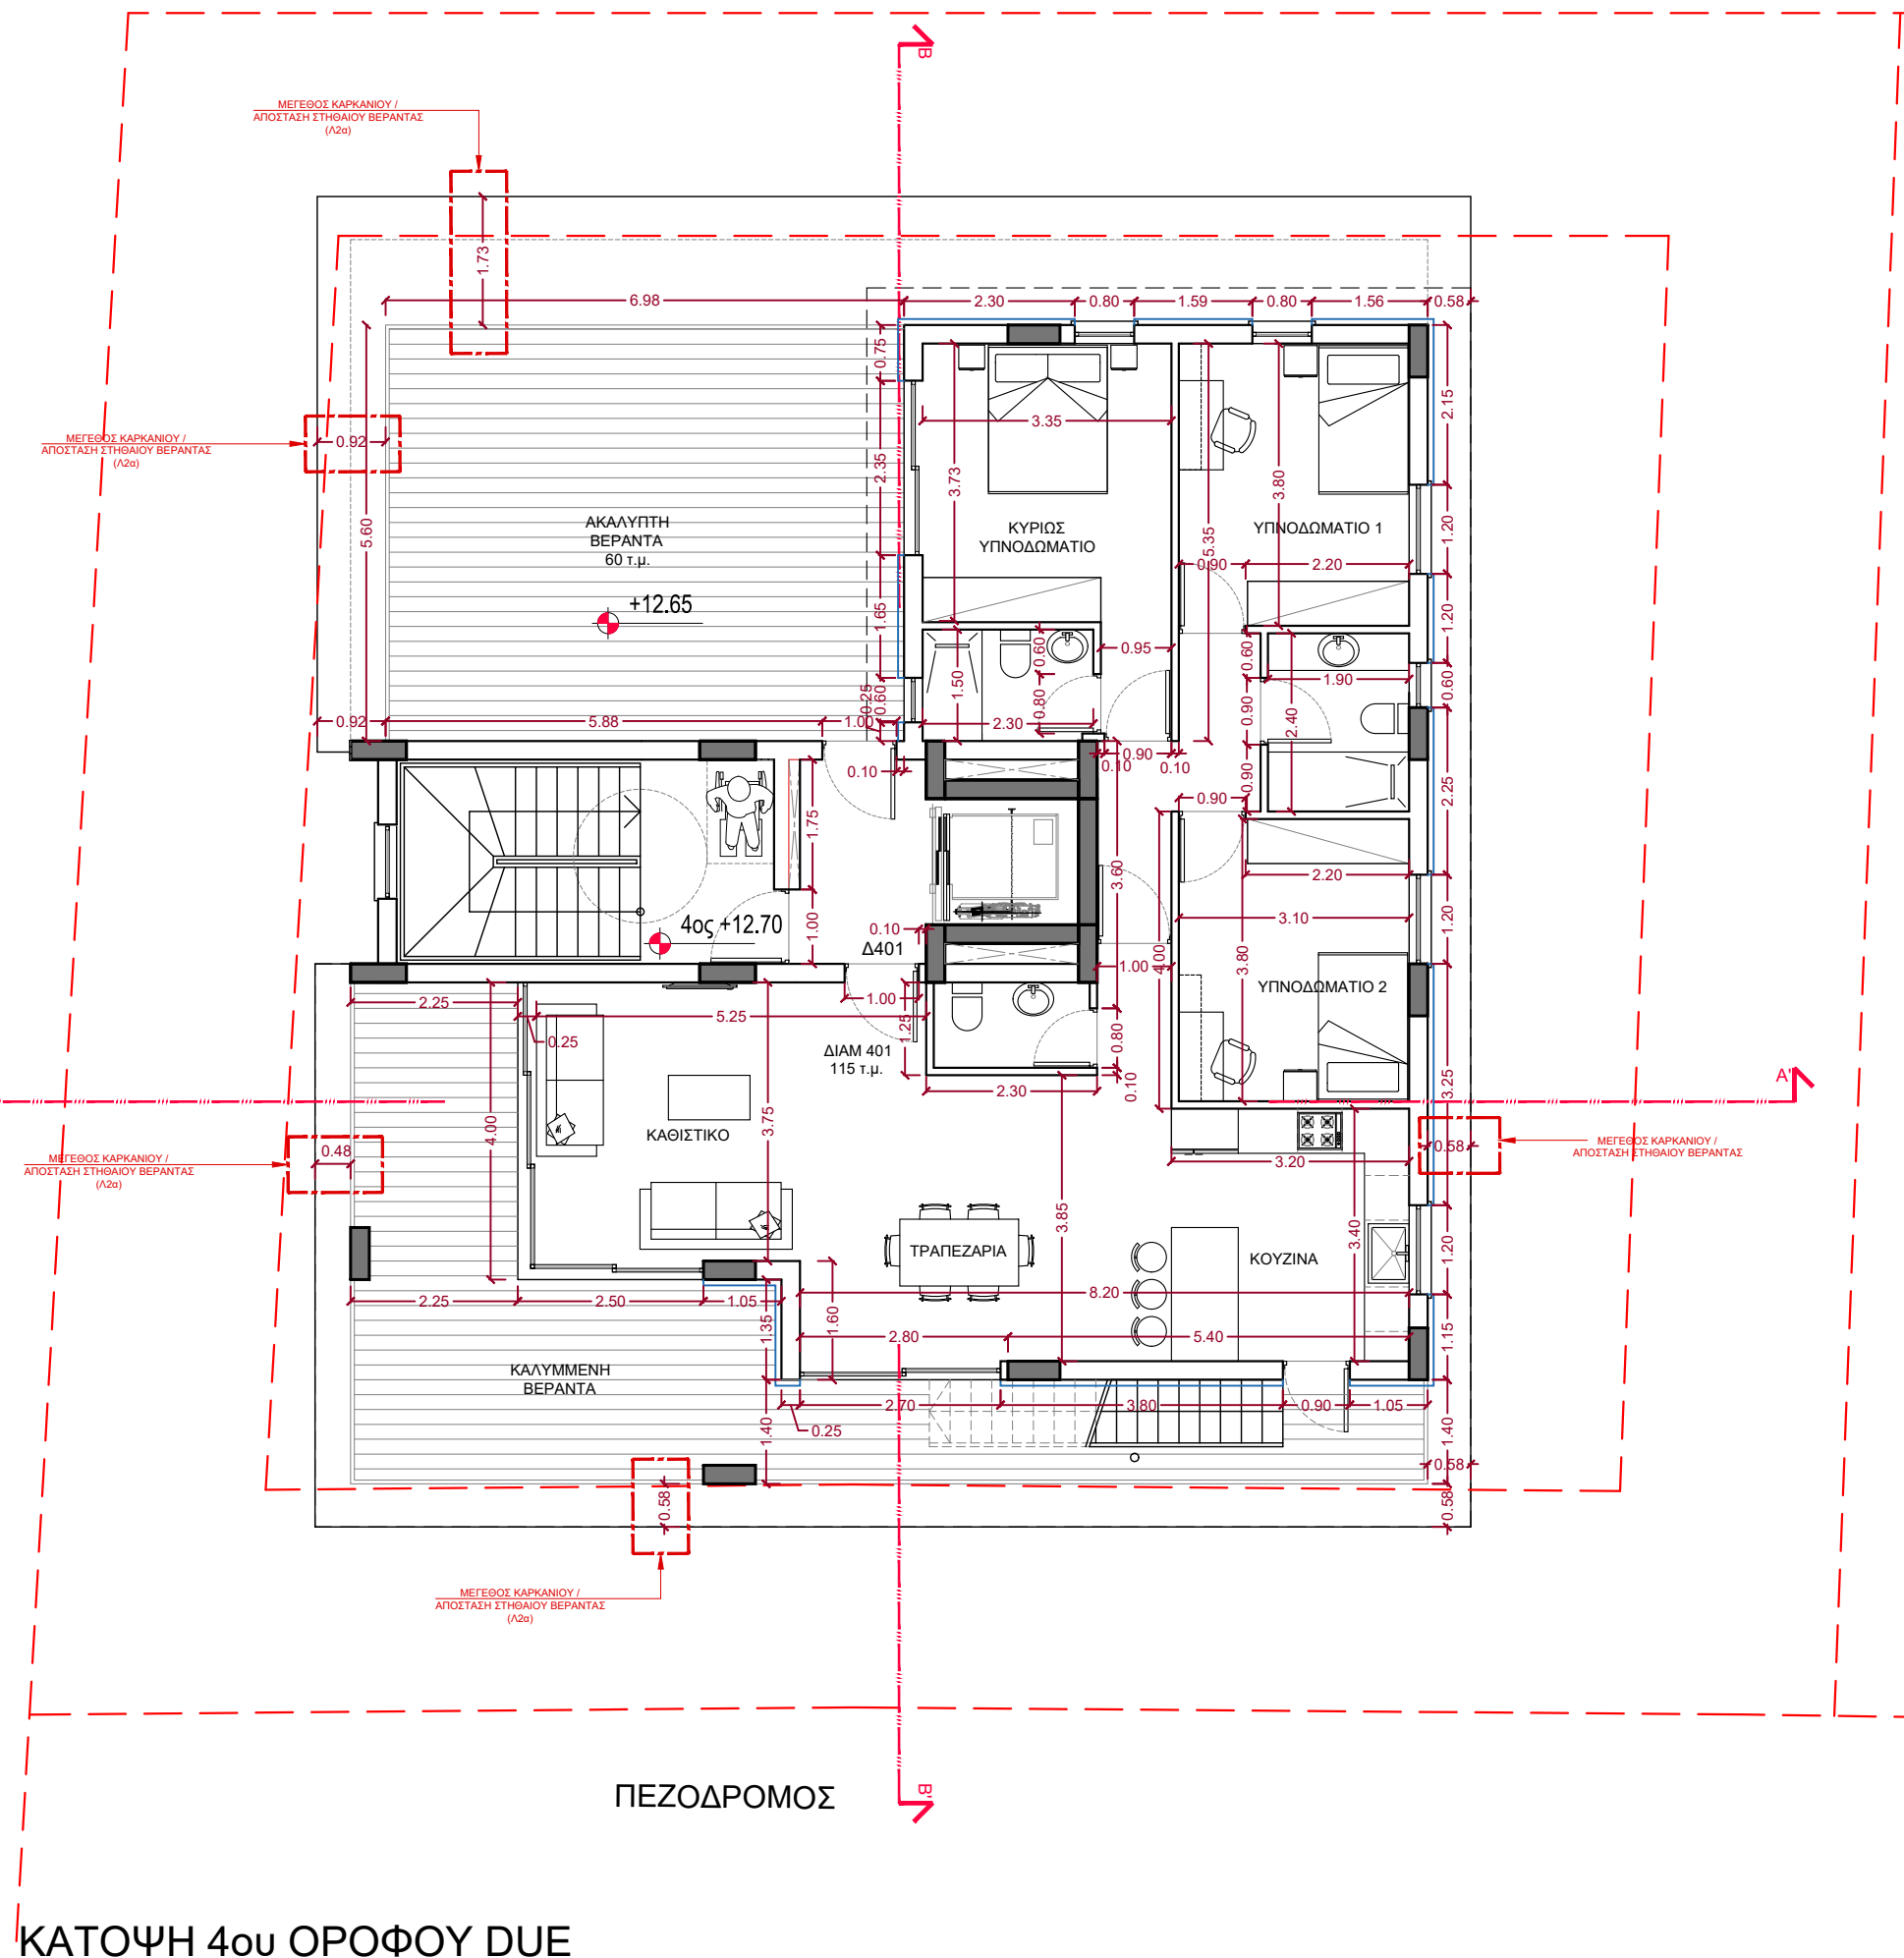

ΚΑΤΟΨΗ 4ου ΟΡΟΦΟΥ DUE



ARKIDEA ARCHITECTS

Marios Georgiou
Architect
BA(Hons) DipArch
Reg. Number 86602

4th, Andrea Assioti Street
2007, Strovolos, Nicosia, Cyprus
Tel : +357-99-665412
email : marios@arkideaarchitects.com

NOTES / REVISIONS

PROJECT NAME

Magnum Opus Due

DRAWING TITLE

ΚΑΤΟΨΗ 4ου

DATE

SCALE

27/01/26

1:100

JOB NUMBER


DRAWING No.

TEMAXIO 1172

A04



ΠΕΖΟΔΡΟΜΟΣ

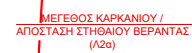


ΜΕΓΕΘΟΣ ΚΑΡΚΑΝΙΟΥ /
ΑΠΟΣΤΑΣΗ ΣΤΗΘΑΙΟΥ ΒΕΡΑΝΤΑΣ
(Λ2α)



4^A, Andrea Assioti Street
2007, Strovolos, Nicosia, Cyprus
Tel : +357-99-665412
email : marios@arkideearchitects.com

NOTES / REVISIONS

TEMAXIO 1172	A05
--------------	-----

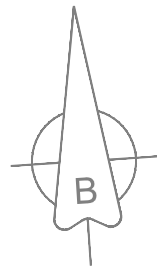

ΔΡΟΜΟΣ

1A

8B

+12.65

+18.70

+15.90

+15.90

8B

ΠΕΖΟΔΡΟΜΟΣ

ΚΑΤΟΨΗ ΟΡΟΦΗΣ ΚΛΙΜΑΚΟΣΤΑΣΙΟΥ DUE



Marios Georgiou
Architect
BA(Hons) DipArch
Reg. Number 86602

4^A, Andrea Assioti Street
2007, Strovolos, Nicosia, Cyprus
Tel : +357-99-665412
email : marios@arkideaarchitects.com

NOTES / REVISIONS

PROJECT NAME

Magnum Opus Due

DRAWING TITLE

ΑΠΟΛΗΞΗ ΚΛΙΜΑΚΟΣΤΑΣΙΟΥ

DATE

27/01/26

JOB NUMBER

TEMAXIO 1172

SCALE

1:100

DRAWING No.

A06



ΠΕΖΟΔΡΟΜΙΟ

εισοδος/εξοδος
οχηματων

εισοδος/εξοδος
οχηματων

ΠΕΖΟΔΡΟΜΟΣ

ΚΑΤΟΨΗ ΙΣΟΓΕΙΟΥ DUE




4^A, Andrea Assioti Street
2007, Strovolos, Nicosia, Cyprus
Tel : +357-99-665412
email : marios@arkideearchitects.com


NOTES / REVISIONS

ΚΑΤΟΨΗ ΙΣΟΓΕΙΟΥ
ΚΑΤΑΛΟΓΟΙ ΑΛΟΥΜ. & ΘΥΡΩΝ

TEMAXIO 1172	K04
--------------	-----

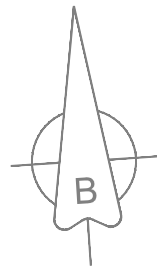

ΔΡΟΜΟΣ

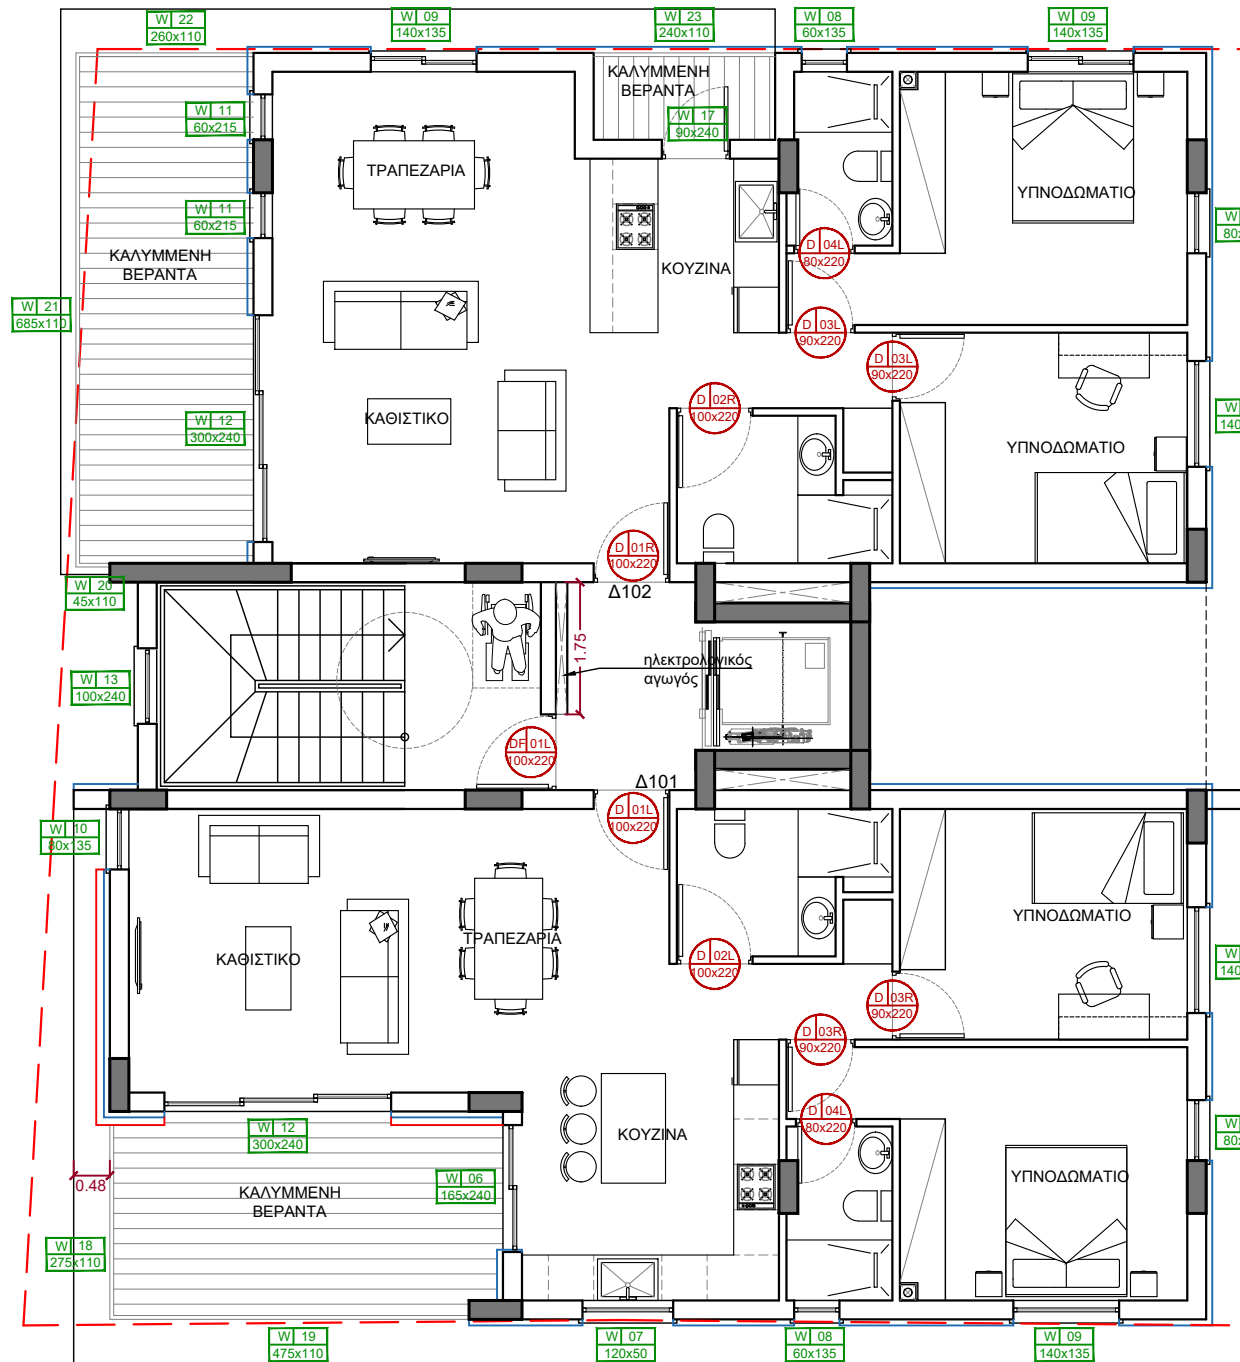

ΠΕΖΟΔΡΟΜΟΣ

ΚΑΤΟΨΗ 1ου ΟΡΟΦΟΥ DUE



ARKIDEA ARCHITECTS

Marios Georgiou
Architect
BA(Hons) DipArch
Reg. Number 86602

4th, Andrea Assioti Street
2007, Strovolos, Nicosia, Cyprus
Tel : +357-99-665412
email : marios@arkideaarchitects.com

NOTES / REVISIONS

PROJECT NAME

Magnum Opus Due

DRAWING TITLE

ΚΑΤΟΨΗ 1ου κ 2ου
ΚΑΤΑΛΟΓΟΙ ΑΛΟΥΜ. & ΘΥΡΩΝ

DATE

SCALE

27/01/26


1:100

JOB NUMBER


DRAWING No.

TEMAXIO 1172

K05

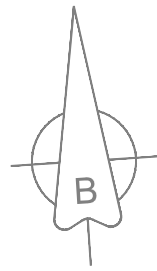

ΔΡΟΜΟΣ

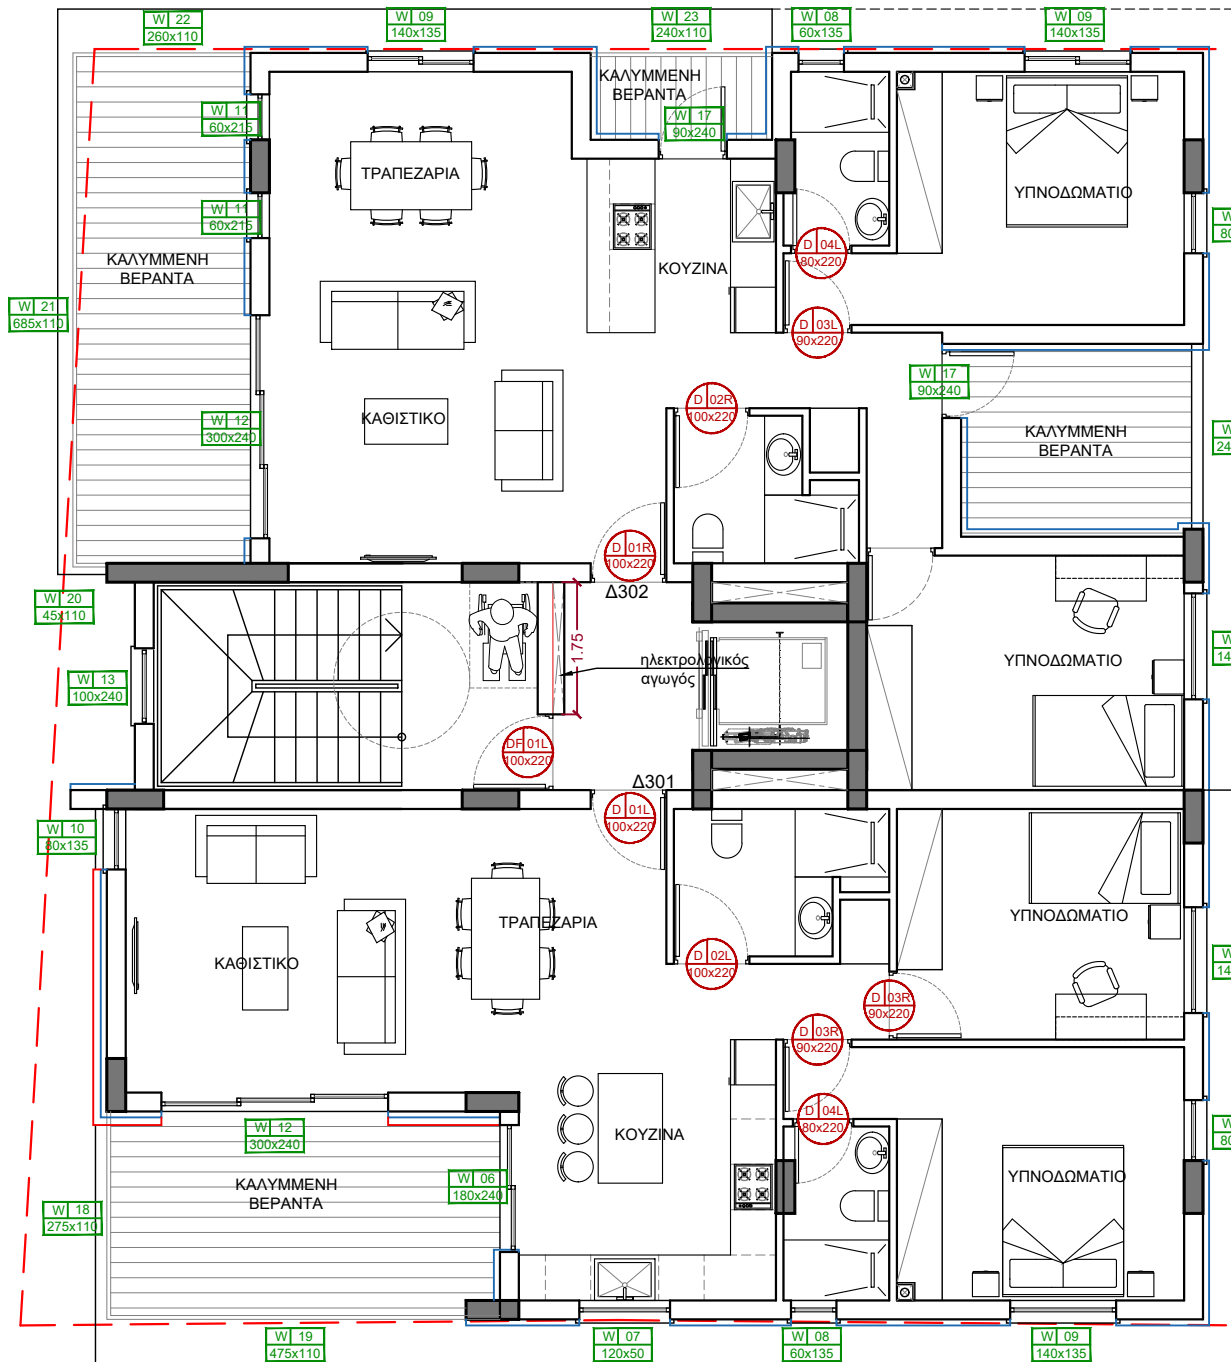

ΠΕΖΟΔΡΟΜΟΣ

ΚΑΤΟΨΗ 3ου ΟΡΟΦΟΥ DUE



ARKIDEA ARCHITECTS

Marios Georgiou
Architect
BA(Hons) DipArch
Reg. Number 86602

4th, Andrea Assioti Street
2007, Strovolos, Nicosia, Cyprus
Tel : +357-99-665412
email : marios@arkideaarchitects.com

NOTES / REVISIONS

PROJECT NAME

Magnum Opus Due

DRAWING TITLE


ΚΑΤΟΨΗ 3ου
ΚΑΤΑΛΟΓΟΙ ΑΛΟΥΜ. & ΘΥΡΩΝ

DATE SCALE


27/01/26 1:100

JOB NUMBER DRAWING No.

TEMAXIO 1172 K06

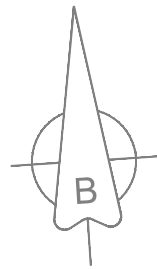

ΔΡΟΜΟΣ

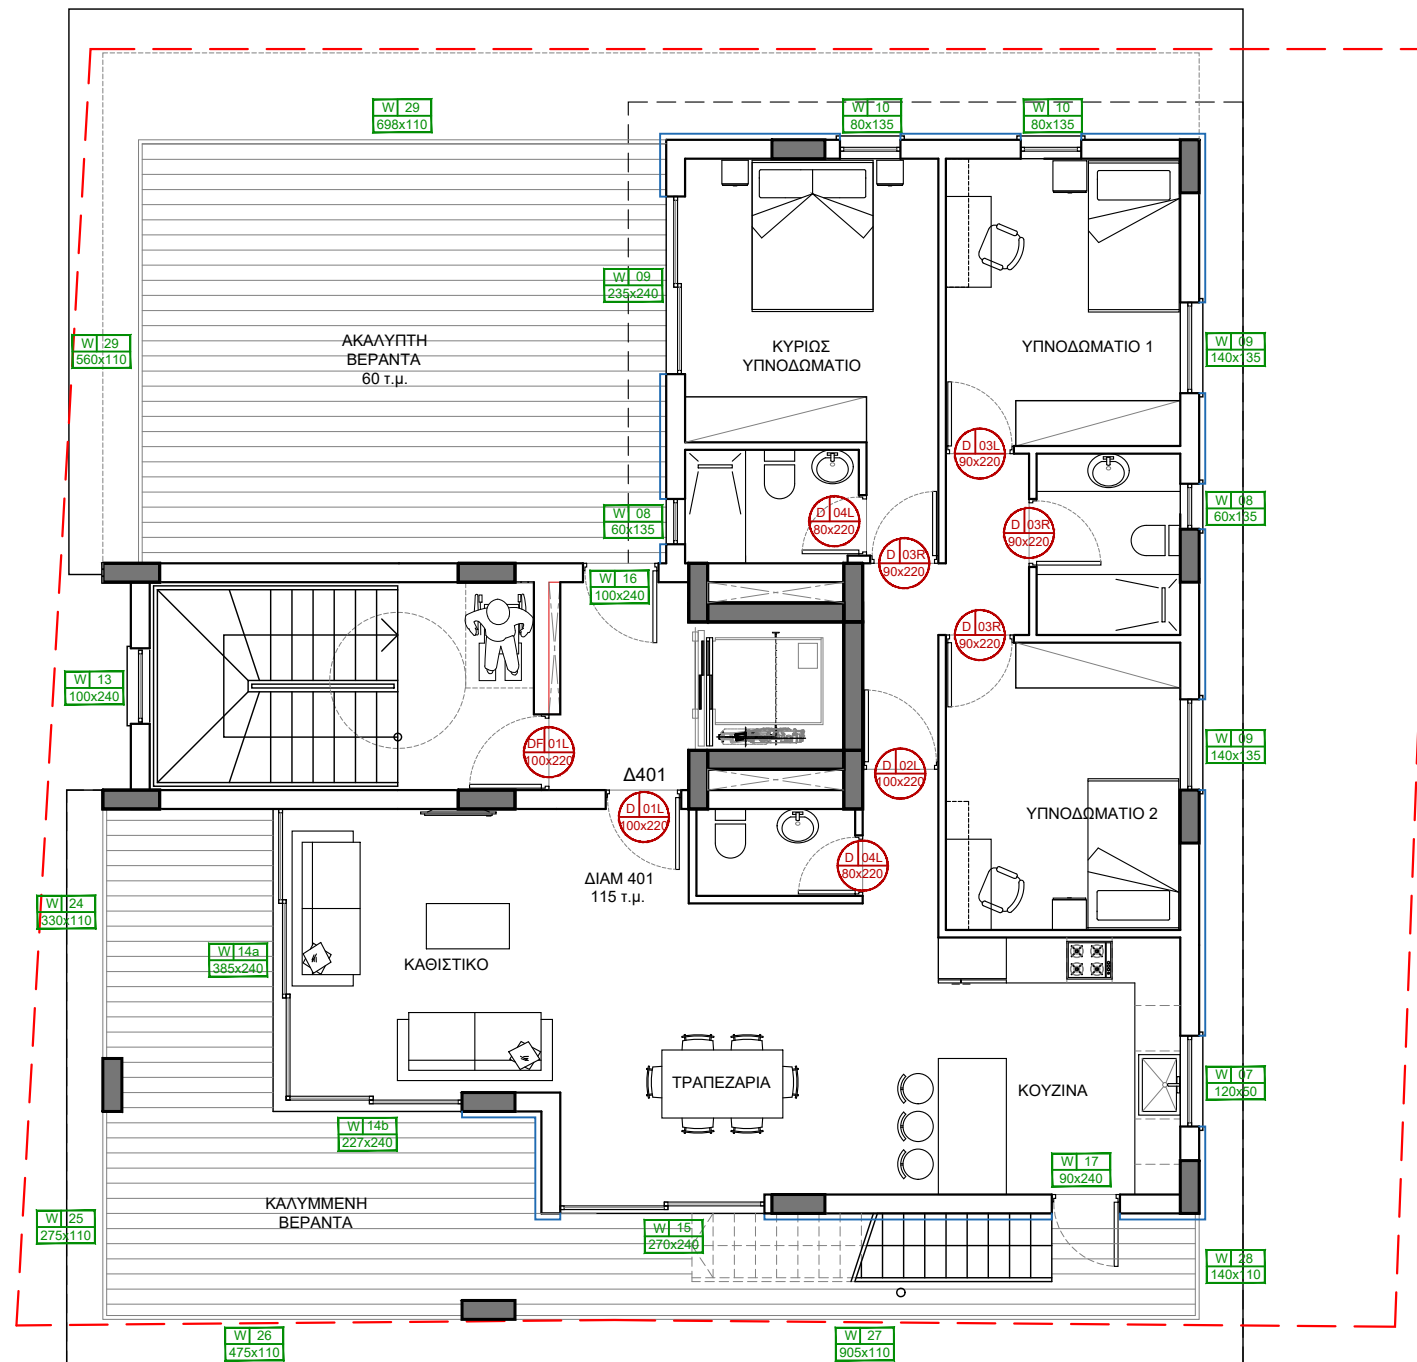

ΠΕΖΟΔΡΟΜΟΣ

ΚΑΤΟΨΗ 4ου ΟΡΟΦΟΥ DUE



ARKIDEA ARCHITECTS

Marios Georgiou
Architect
BA(Hons) DipArch
Reg. Number 86602

4th, Andrea Assioti Street
2007, Strovolos, Nicosia, Cyprus
Tel : +357-99-665412
email : marios@arkideaarchitects.com

NOTES / REVISIONS

PROJECT NAME

Magnum Opus Due

DRAWING TITLE

ΚΑΤΟΨΗ 4ου
ΚΑΤΑΛΟΓΟΙ ΑΛΟΥΜ. & ΘΥΡΩΝ

DATE	SCALE
27/01/26	1:100
JOB NUMBER	DRAWING No.
TEMAXIO 1172	K07



4^A, Andrea Assiotti Street
2007, Strovolos, Nicosia, Cyprus
Tel : +357-99-665412
email : marios@arkideearchitects.com

NOTES / REVISIONS

ΚΑΤΟΨΗ ΟΡΟΦΗΣ

K08