

ΔΡΟΜΟΣ



ARKIDEA ARCHITECTS

Marios Georgiou
Architect
BA(Hons) DipArch
Reg. Number 86602

4^A, Andrea Assiotti Street
2007, Strovolos, Nicosia, Cyprus
Tel : +357-99-665412
email : marios@arkideearchitects.com

NOTES / REVISIONS

[illegible]

PROJECT NAME

Magnum Opus Tre



DRAWING TITLE

ΚΑΤΟΨΗ 1ου

DATE	SCALE
27/01/26	1:100
JOB NUMBER	DRAWING No.
TEMAXIO 1173	B01

ΠΕΖΟΔΡΟΜΟΣ

ΚΑΤΟΨΗ 1ου ΟΡΟΦΟΥ ΤRΕ

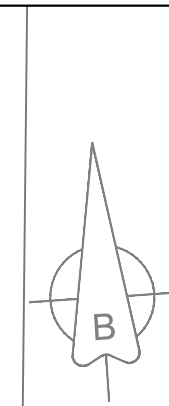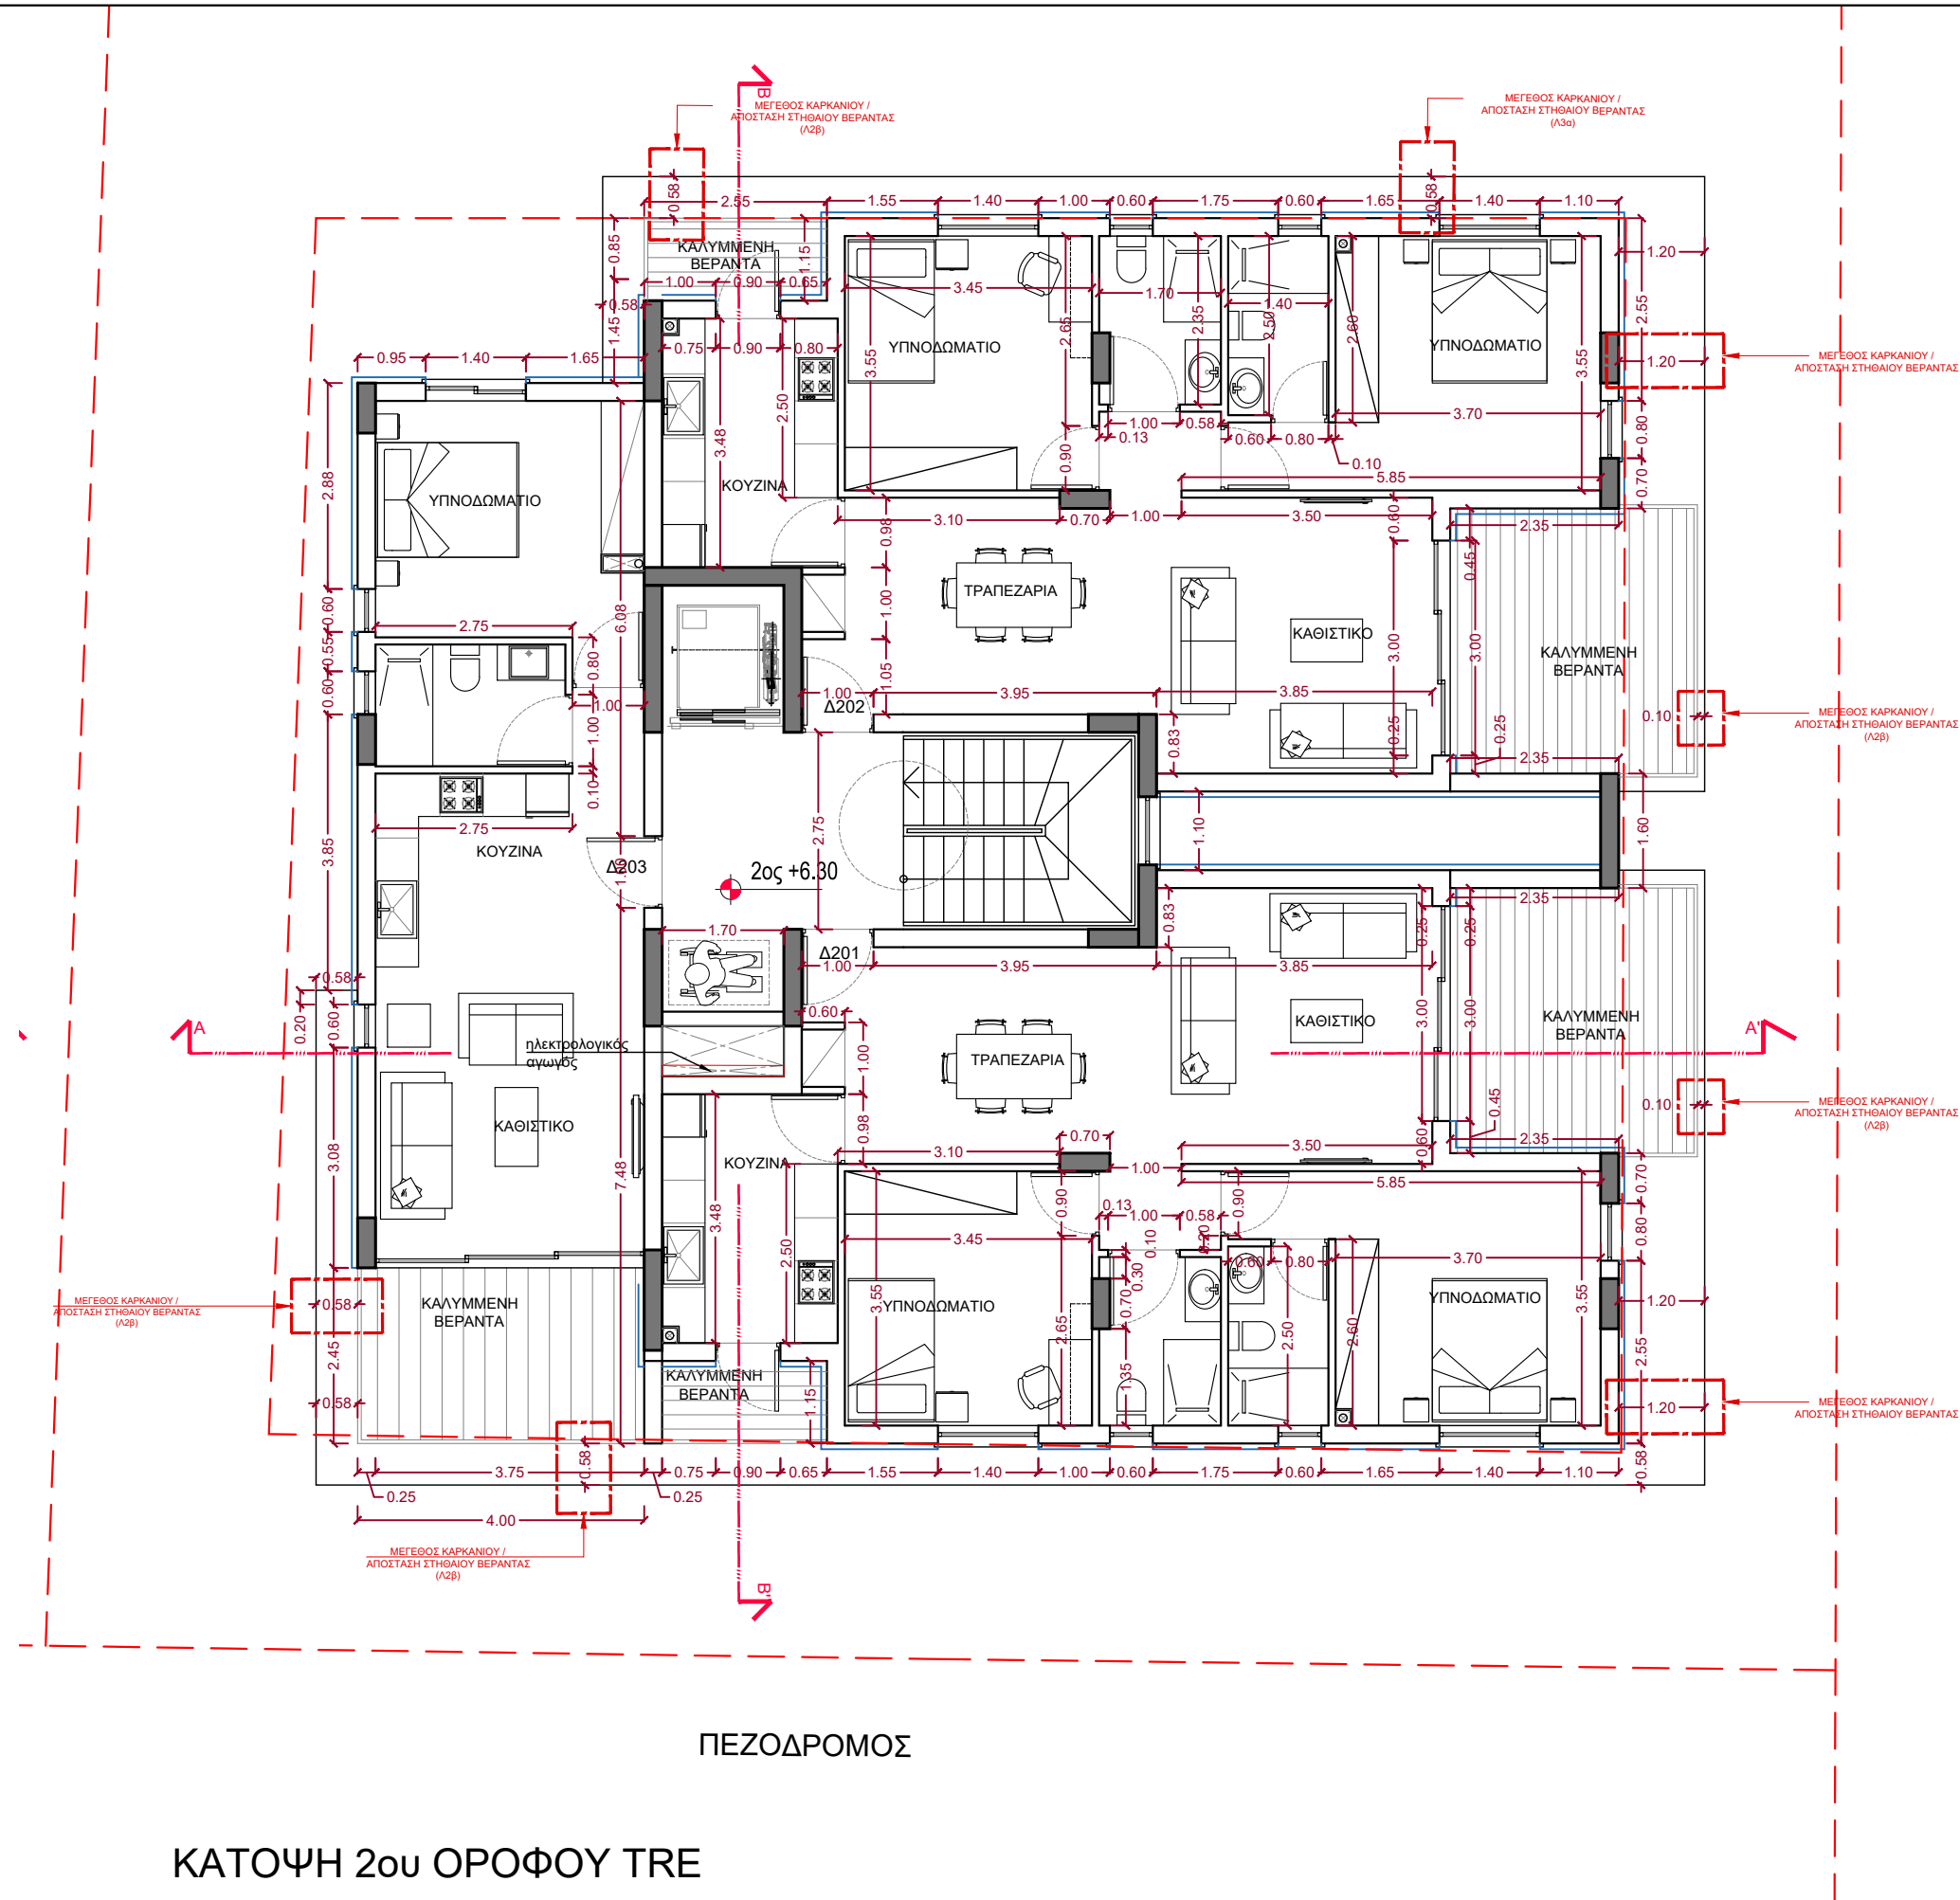

ΔΡΟΜΟΣ

ΚΑΤΟΨΗ 2ου ΟΡΟΦΟΥ TRE



ARKIDEA ARCHITECTS

Marios Georgiou
Architect
BA(Hons) DipArch
Reg. Number 86602

4th, Andrea Assioti Street
2007, Strovolos, Nicosia, Cyprus
Tel : +357-99-665412
email : marios@arkideaarchitects.com

NOTES / REVISIONS


PROJECT NAME

Magnum Opus Tre



DRAWING TITLE

ΚΑΤΟΨΗ 2ου

DATE	SCALE
27/01/26	1:100
JOB NUMBER	DRAWING No.
TEMAXIO 1173	B02

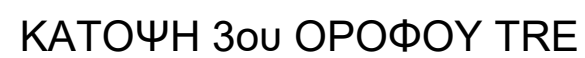

B03

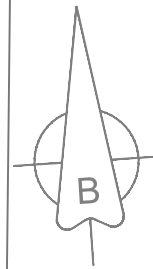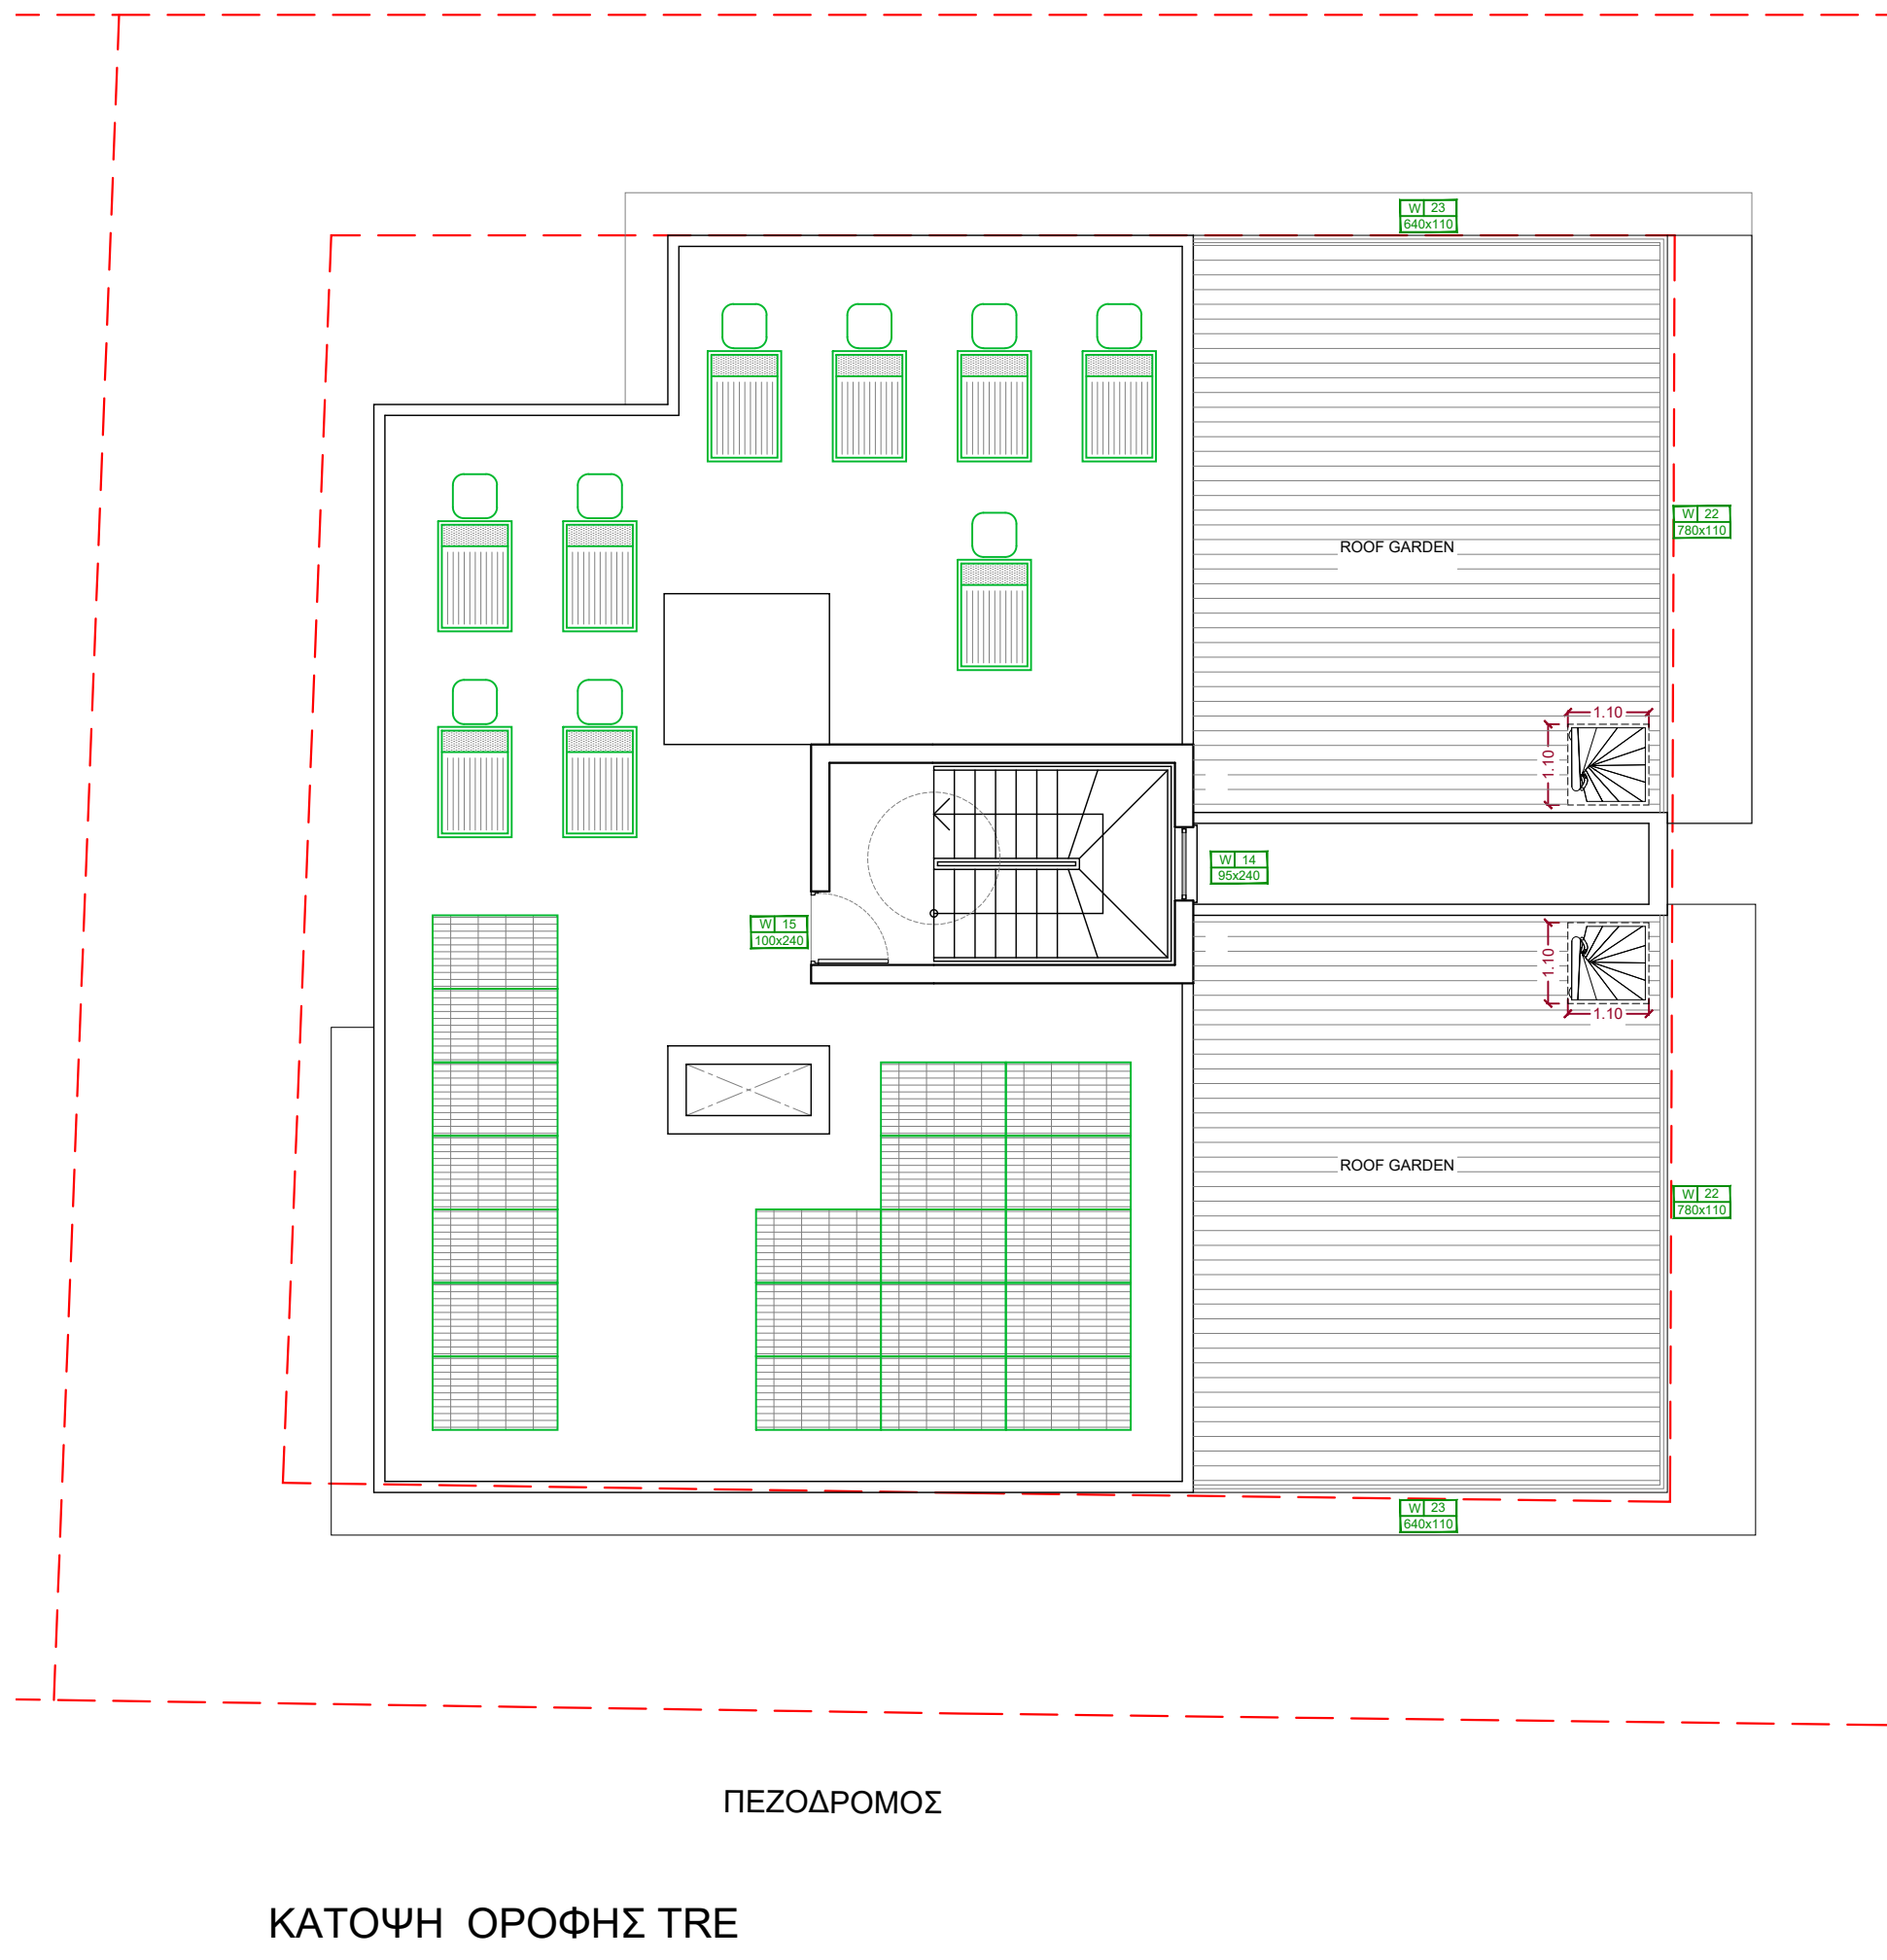

Marios Georgiou
Architect
BA(Hons) DipArch
Reg. Number 86602

NOTES / REVISIONS

PROJECT NAME	
Magnum Opus Tre	
DRAWING TITLE	
ΚΑΤΟΨΗ ΟΡΟΦΗΣ	
ΚΑΤΑΛΟΓΟΙ ΑΛΟΥΜ & ΘΥΡΩΝ	
DATE	SCALE
27/01/26	1:100
JOB NUMBER	DRAWING No.
TEMAXIO 1173	K07