


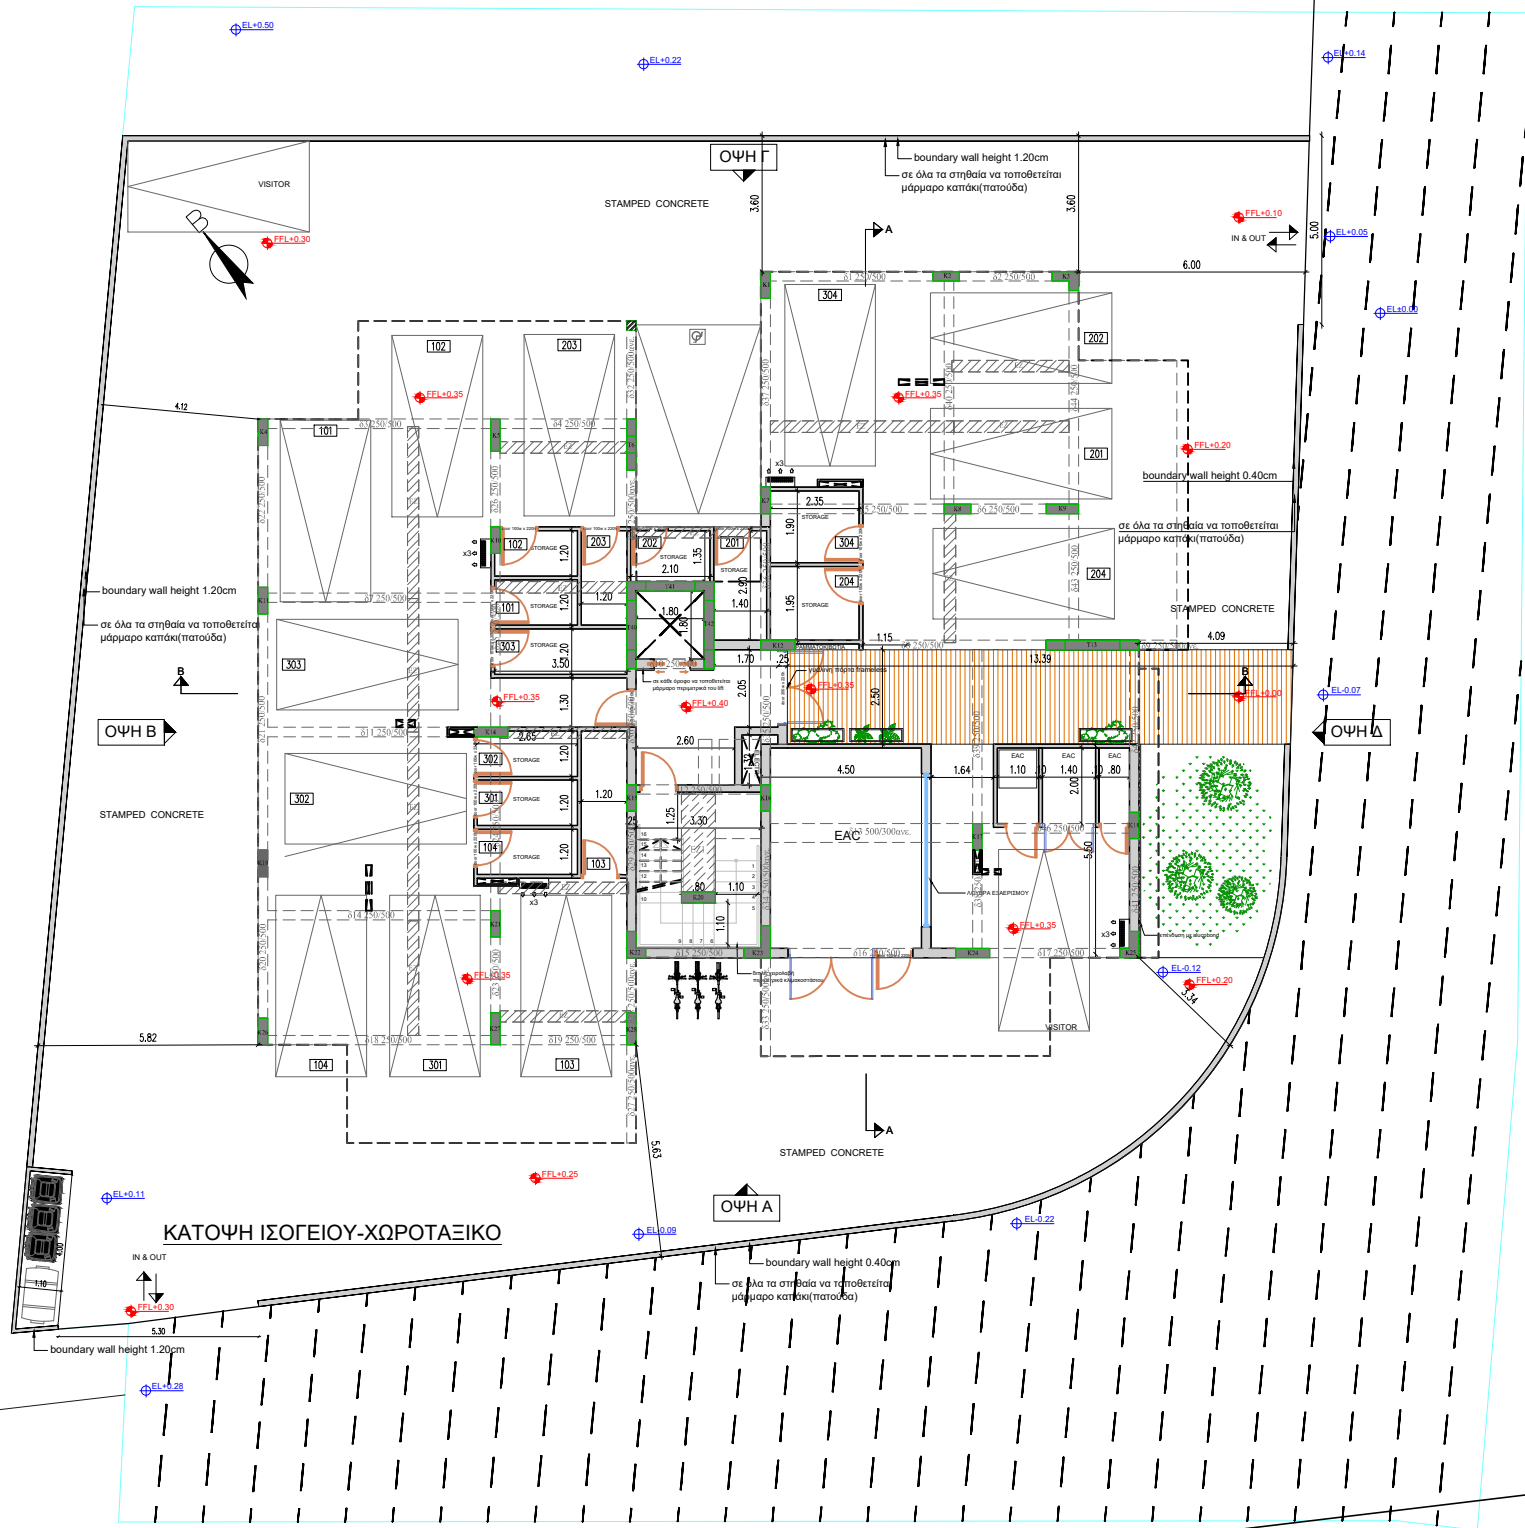

NOTES :

1. ΟΛΑ ΤΑ ΥΛΙΚΑ ΝΑ ΧΡΗΣΙΜΟΠΟΙΗΘΟΥΝ ΜΕ ΤΗ ΣΥΓΚΑΤΑΘΕΣΗ ΤΟΥ ΑΡΧΙΤΕΚΤΟΝΑ.
2. ΟΛΑ ΤΑ ΑΡΧΙΤΕΚΤΟΝΙΚΑ ΣΧΕΔΙΑ ΚΑΙ ΛΕΠΤΟΜΕΡΕΙΕΣ ΝΑ ΔΙΑΒΑΖΟΝΤΑΙ ΜΑΖΙ ΜΕ ΤΑ ΣΤΑΤΙΚΑ & ΗΛΕΚΤΡΟΜΗΧΑΝΟΛΟΓΙΚΑ ΣΧΕΔΙΑ. ΓΙΑ ΟΠΟΙΕΣΔΗΠΟΤΕ ΔΙΑΦΟΡΕΣ ΝΑ ΕΝΗΜΕΡΩΝΕΤΑΙ Ο ΕΠΙΒΛΕΠΩΝ ΤΟΥ ΕΡΓΟΥ.
3. ΟΙ ΔΙΑΣΤΑΣΕΙΣ ΤΩΝ ΚΟΥΟΝΕΝΟΜΑΤΩΝ ΣΤΑ ΑΡΧΙΤΕΚΤΟΝΙΚΑ ΕΙΝΑΙ ΚΑΘΑΡΕΣ. Ο ΕΡΓΟΛΑΒΟΣ ΕΙΝΑΙ ΥΠΟΧΡΕΩΣ ΝΑ ΚΑΤΑΣΚΕΥΑΣΗ ΤΑ ΚΟΥΟΝΕΝΩΜΑΤΑ ΛΑΜΒΑΝΟΝΤΑΣ ΥΠΟΦ.Η 3 ΧΕΡΙΑ ΣΟΥΒΑ ΚΑΙ ΠΟΛΥΣΤΕΡΙΝΗ ΚΑΙ ΟΠΟΙΟΔΗΠΟΤΕ ΤΕΛΙΚΟ ΕΠΙΧΡΙΣΜΑ.

D.W = ΠΛΥΝΤΗΡΙΟ ΠΙΑΤΩΝ
W.M = ΠΛΥΝΤΗΡΙΟ ΡΟΥΧΩΝ
Σ.Ρ = ΣΤΕΓΝΩΤΗΡΙΟ ΡΟΥΧΩΝ
F.. = F.ΥΓΕΙΟ
OVEN. = ΟΥΕΝΟΥΡΝΟΣ

BY :	DATE :	REVISION :
-	-	-
-	-	-
-	-	-
-	-	-
-	-	-
-	-	-
-	-	-
-	-	-
-	-	-
-	-	-

EL = EXISTING LEVEL
YOVENISTAMENO YF.OMETPO
ERL = EXISTING ROAD LEVEL
YOVENISTAMENO YF.OMETPO ΔΡΟΜΟΥ
EPL = EXISTING PAVEMENT LEVEL
YOVENISTAMENO YF.OMETPO ΠΕΖΟΔΡΟΜΙΟΥ

PGL = PROPOSED GROUND LEVEL
ΠΡΟΤΕΙΝΟΜΕΝΟ YF.OMETPO ΕΔΑΦΟΝΟΥΣ
FFL = FINISHED FLOOR LEVEL
YF.OMETPO ΤΕΛΕΙΩΜΕΝΟΥ ΠΙΑΤΩΜΑΤΟΣ
SSL = STRUCTURAL SLAB LEVEL
ΔΟΜΙΚΟ YF.OMETPO ΠΛΑΚΑΣ
TOB = TOP OF BEAM
TOP = TOP OF PARAPET
ΔΟΜΙΚΟ YF.OMETPO ΠΛΑΤΩ ΜΕΡΟΥΣ ΔΟΚΟΥ
ΔΟΜΙΚΟ YF.OMETPO ΠΛΑΤΩ ΜΕΡΟΥΣ ΣΤΗΘΑΙΟΥ

CODE ARCHITECTURE STUDIO
ARCHITECTS & ENGINEERS

MICHALIS NEOFYTOU
ARCHITECT N.T.U.A.-MA ARCHITECTURE

ΜΙΧΑΛΗΣ ΝΕΟΦΥΤΟΥ
ΑΡΧΙΤΕΚΤΟΝΑΣ
ΕΜΠ - MA ARCHITECTURE
A.M.: A116407

ΑΓΙΟΥ ΑΝΤΟΝΙΟΥ 6
NIKA TOWER FLAT 202
7102, ARADIPPOY
LARNACA-CYPRUS
TEL. 24534204 FAX. 24323019
EMAIL INFO@CA-STUDIO.COM

JOB TITLE : ΠΟΛΥΚΑΤΟΙΚΙΑ 12 ΔΙΑΜΕΡΙΣΜΑΤΩΝ

OWNER : DEXTEK CONTRACTORS LIMITED


SHEET TITLE : ΚΑΤΟΨΗ ΧΩΡΟΤΑΞΙΚΟΥ

DATE : ΔΕΚΕΜΒΡΙΟΣ 2024

A 01

SCALE : 1 : 100 @ A3

DESIGN	JOB NO
T.R	594

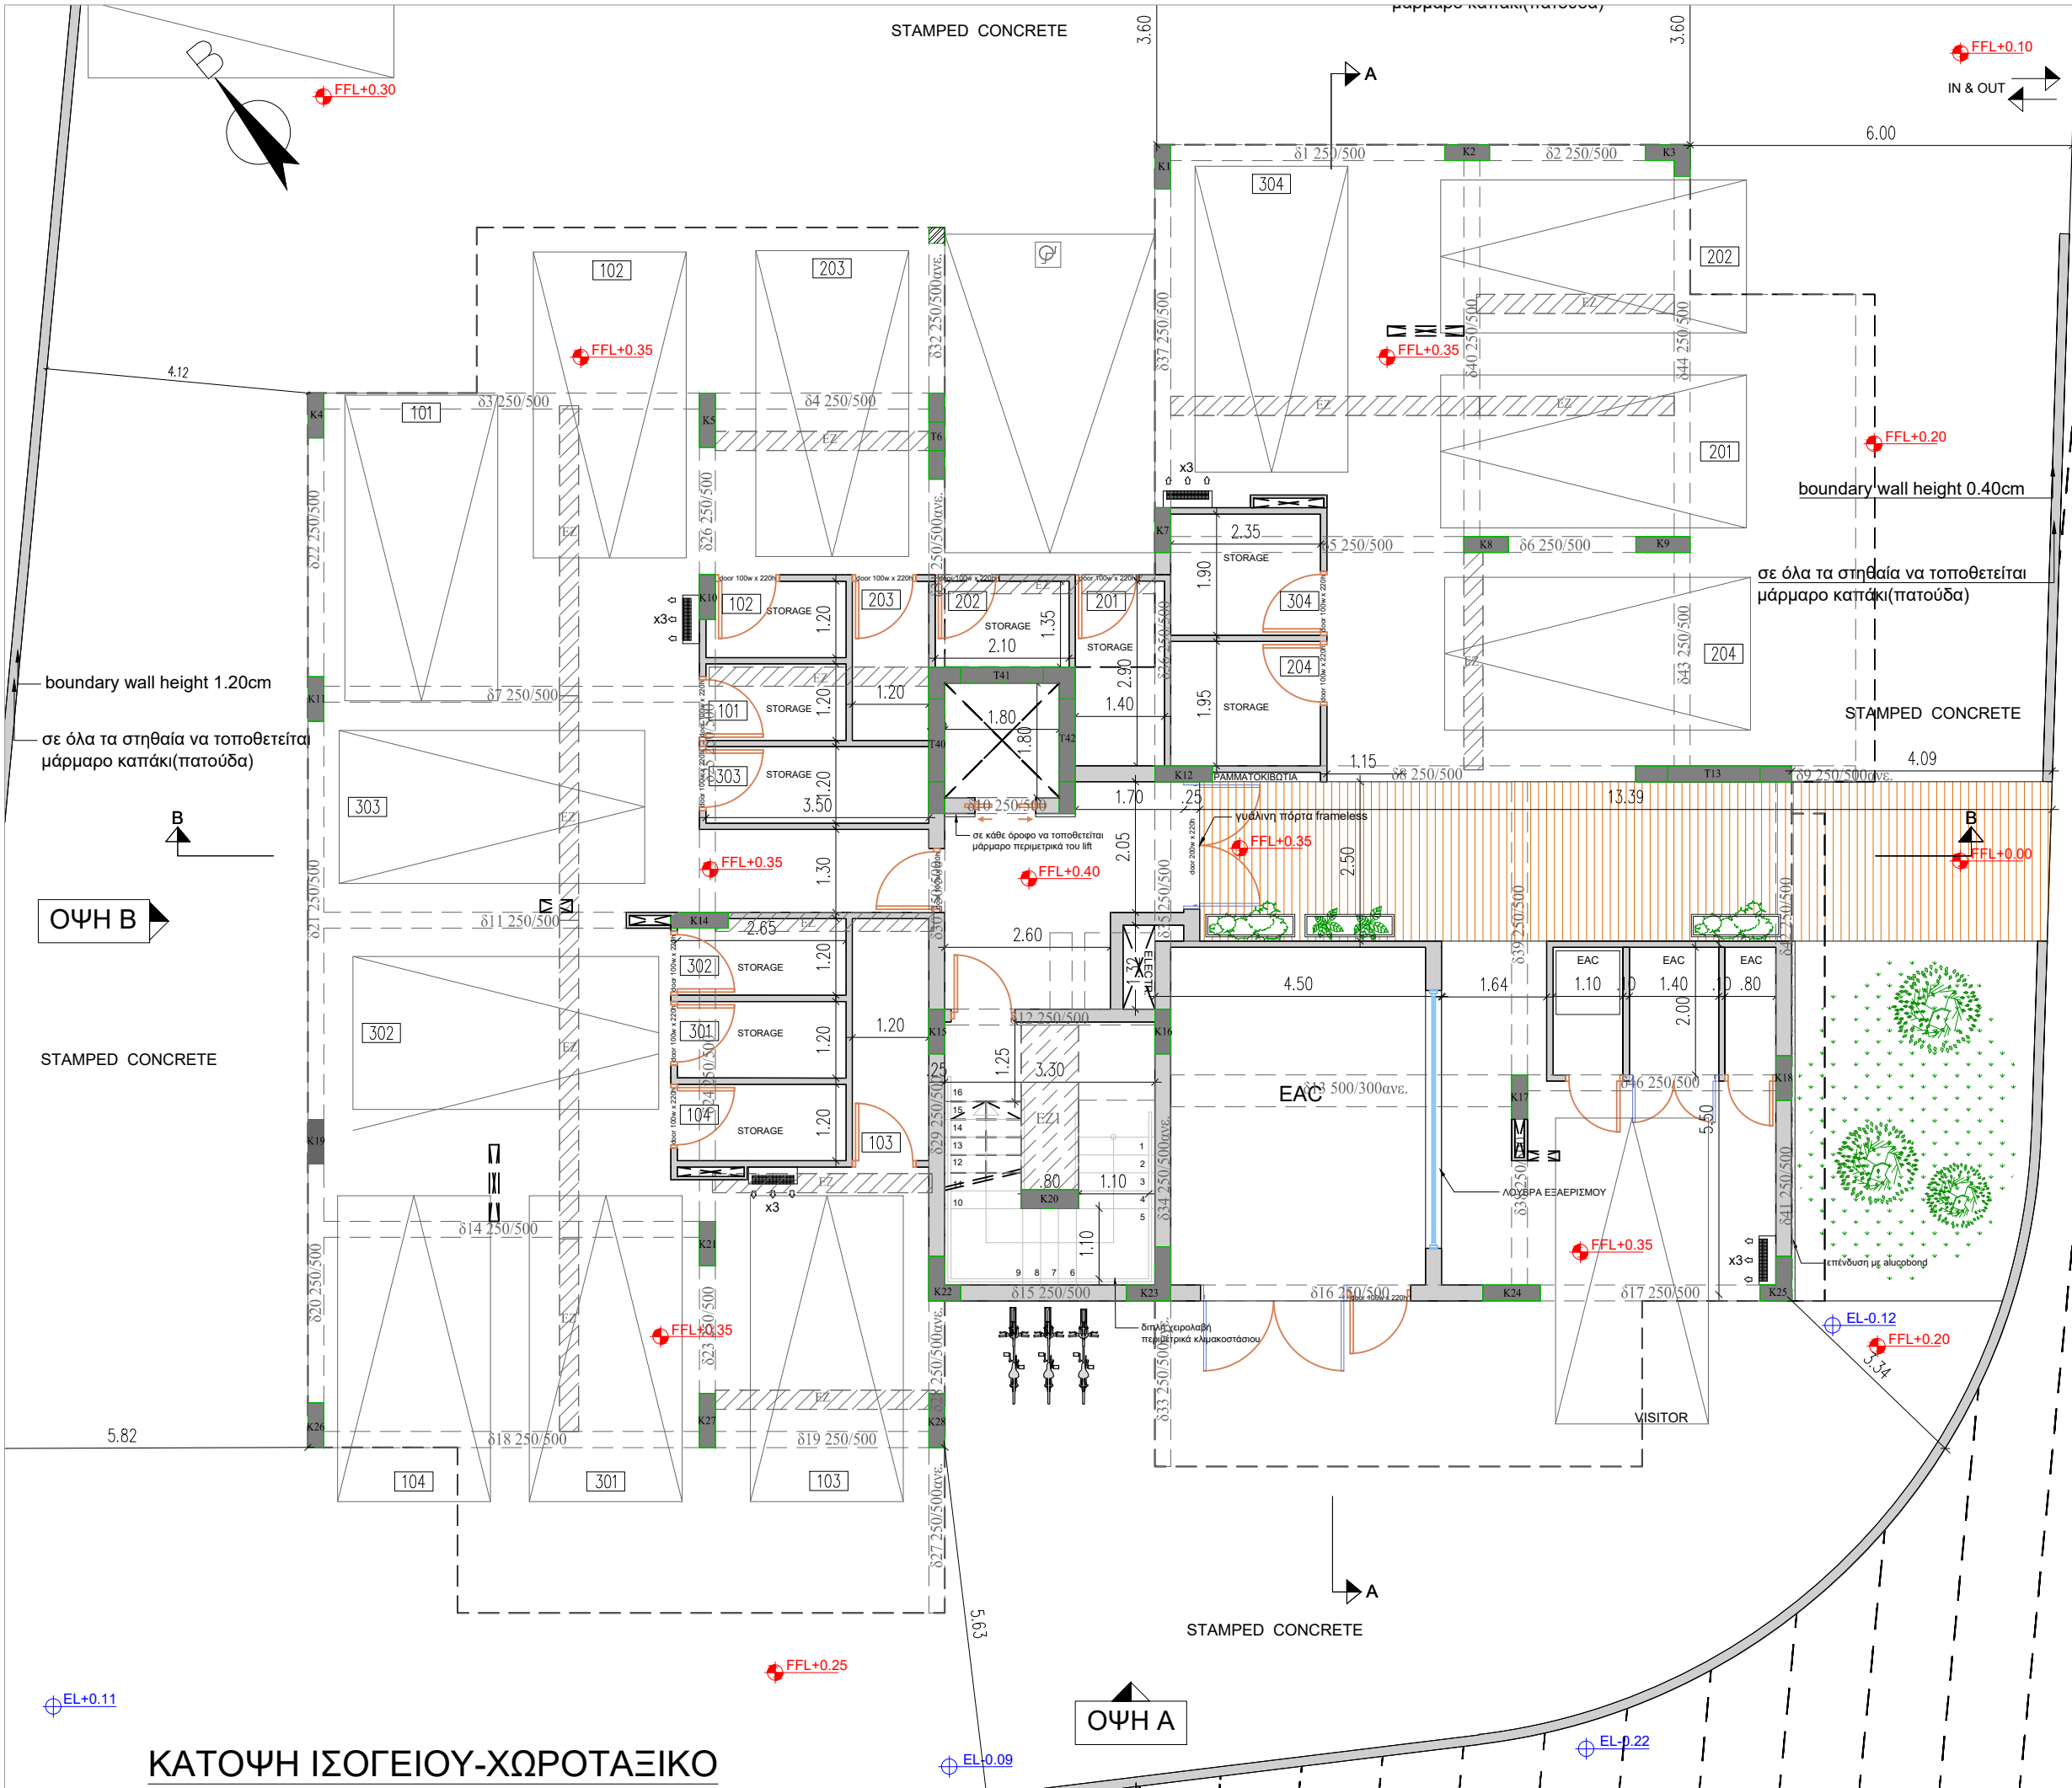

NOTES :

1. ΟΛΑ ΤΑ ΥΛΙΚΑ ΝΑ ΧΡΗΣΙΜΟΠΟΙΗΘΟΥΝ ΜΕ ΤΗ ΣΥΓΚΑΤΑΘΕΣΗ ΤΟΥ ΑΡΧΙΤΕΚΤΟΝΑ.

2. ΟΛΑ ΤΑ ΑΡΧΙΤΕΚΤΟΝΙΚΑ ΣΧΕΔΙΑ ΚΑΙ ΛΕΠΤΟΜΕΡΕΙΕΣ ΝΑ ΔΙΑΒΑΖΟΝΤΑΙ ΜΑΖΙ ΜΕ ΤΑ ΣΤΑΤΙΚΑ & ΗΛΕΚΤΡΟΜΗΧΑΝΟΛΟΓΙΚΑ ΣΧΕΔΙΑ. ΓΙΑ ΟΠΟΙΕΣΔΗΠΟΤΕ ΔΙΑΦΕΡΟΝΤΕΣ ΝΑ ΕΝΗΜΕΡΩΝΕΤΑΙ Ο ΕΠΙΒΛΕΠΩΝ ΤΟΥ ΕΡΓΟΥ.

3. ΟΙ ΔΙΑΣΤΑΣΕΙΣ ΤΩΝ ΚΟΥΟΝΕΝΟΜΑΤΩΝ ΣΤΑ ΑΡΧΙΤΕΚΤΟΝΙΚΑ ΕΙΝΑΙ ΚΑΘΑΡΕΣ. Ο ΕΡΓΟΛΑΒΟΣ ΕΙΝΑΙ ΥΠΟΧΡΕΩΣ ΝΑ ΚΑΤΑΣΚΕΥΑΣΗ ΤΑ ΚΟΥΟΝΕΝΩΜΑΤΑ ΛΑΜΒΑΝΟΝΤΑΣ ΥΠΟΨΗ 3 ΧΕΡΙΑ ΣΟΥΒΑ ΚΑΙ ΠΟΛΥΣΤΕΡΙΝΗ ΚΑΙ ΟΠΟΙΟΔΗΠΟΤΕ ΤΕΛΙΚΟ ΕΠΙΧΡΙΣΜΑ.

D.W = ΠΛΥΝΤΗΡΙΟ ΠΙΑΤΩΝ
W.M = ΠΛΥΝΤΗΡΙΟ ΡΟΥΧΩΝ
Σ.Ρ = ΣΤΕΓΝΩΤΗΡΙΟ ΡΟΥΧΩΝ
F.. = Φ.ΥΓΕΙΟ
OVEN. = ΟΥΕΝΟΥΡΝΟΣ

BY :	DATE :	REVISION :
-	-	-
-	-	-
-	-	-
-	-	-
-	-	-
-	-	-
-	-	-
-	-	-
-	-	-
-	-	-
-	-	-

EL = EXISTING LEVEL
YOVENISTAMENO YF. OMETPO
ERL = EXISTING ROAD LEVEL
EPL = EXISTING PAVEMENT LEVEL
YOVENISTAMENO YF. OMETPO ΔΡΟΜΟΥ
YOVENISTAMENO YF. OMETPO ΠΕΖΟΔΡΟΜΙΟΥ

PGL = PROPOSED GROUND LEVEL
PTEINOMENO YF. OMETPO EDAOYENOYΣ
FFL = FINISHED FLOOR LEVEL
YF. OMETPO TEΛΕΙΩΜΕΝΟΥ ΠΑΤΩΜΑΤΟΣ
SSL = STRUCTURAL SLAB LEVEL
ΔΟΜΙΚΟ YF. OMETPO ΠΛΑΚΑΣ
TOB = TOP OF BEAM
ΔΟΜΙΚΟ YF. OMETPO ΠΛΑΤΩ ΜΕΡΟΥΣ ΔΟΚΟΥ
TOP = TOP OF PARAPET
ΔΟΜΙΚΟ YF. OMETPO ΠΛΑΤΩ ΜΕΡΟΥΣ ΣΤΗΘΑΙΟΥ

CODE ARCHITECTURE STUDIO
ARCHITECTS & ENGINEERS

MICHALIS NEOFYTOU
ARCHITECT N.T.U.A.-MA ARCHITECTURE

ΜΙΧΑΛΗΣ ΝΕΟΦΥΤΟΥ
ΑΡΧΙΤΕΚΤΟΝΑΣ
EMP - MA ARCHITECTURE
A.M.: A116407


ΑΓΙΟΥ ΑΝΤΩΝΙΟΥ 6
NIKA TOWER FLAT 202
7102, ARADIPPOY
LARNACA-CYPRUS
TEL. 24534204 FAX. 24323019
EMAIL INFO@CA-STUDIO.COM

JOB TITLE : ΠΟΛΥΚΑΤΟΙΚΙΑ 12 ΔΙΑΜΕΡΙΣΜΑΤΩΝ

OWNER : DEXTEK CONTRACTORS LIMITED

SHEET TITLE : ΚΑΤΟΠΗ ΙΣΟΓΕΙΟΥ

DATE : ΔΕΚΕΜΒΡΙΟΣ 2024	A 02
SCALE : 1 : 100 @ A3	DESIGN T.R JOB NO 594

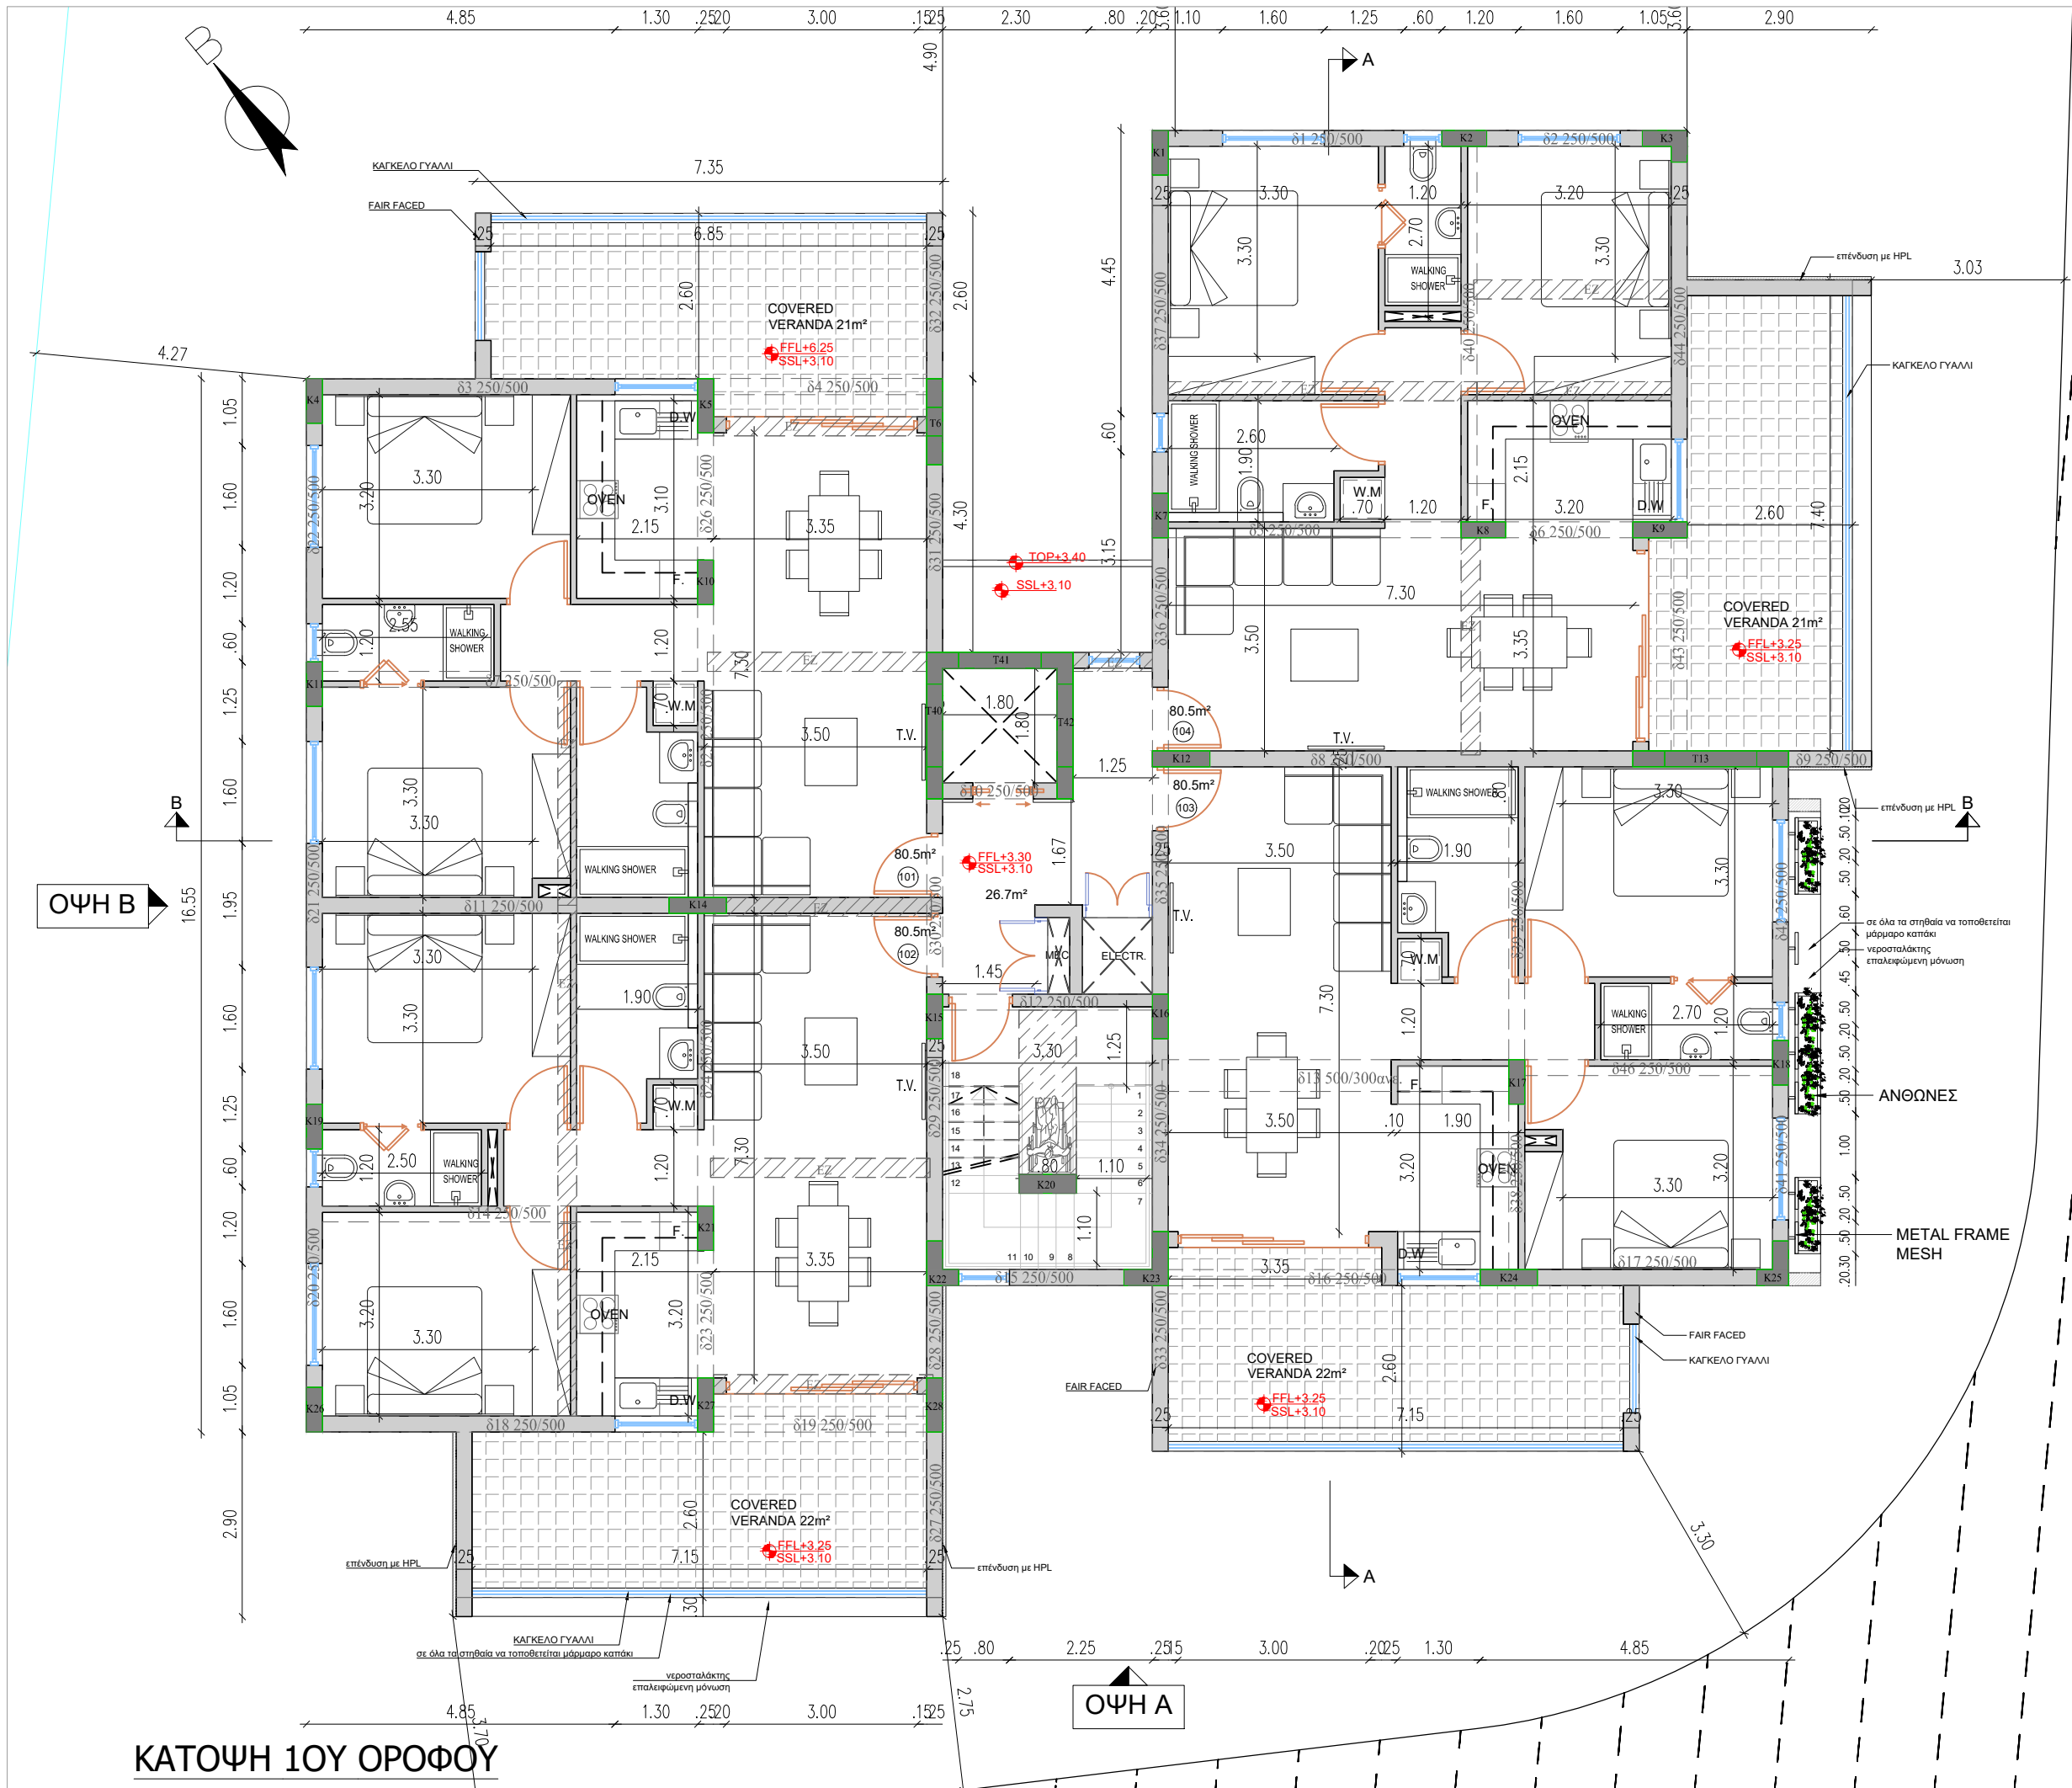

NOTES :

1. ΟΛΑ ΤΑ ΥΛΙΚΑ ΝΑ ΧΡΗΣΙΜΟΠΟΙΗΘΟΥΝ ΜΕ ΤΗ ΣΥΓΚΑΤΑΘΕΣΗ ΤΟΥ ΑΡΧΙΤΕΚΤΟΝΑ.
2. ΟΛΑ ΤΑ ΑΡΧΙΤΕΚΤΟΝΙΚΑ ΣΧΕΔΙΑ ΚΑΙ ΛΕΠΤΟΜΕΡΕΙΕΣ ΝΑ ΔΙΑΒΑΖΟΝΤΑΙ ΜΑΖΙ ΜΕ ΤΑ ΣΤΑΤΙΚΑ & ΗΛΕΚΤΡΟΜΗΧΑΝΟΛΟΓΙΚΑ ΣΧΕΔΙΑ. ΓΙΑ ΟΠΟΙΕΣΔΗΠΟΤΕ ΔΙΑΦΟΡΕΣ ΝΑ ΕΝΗΜΕΡΩΝΕΤΑΙ Ο ΕΠΙΒΛΕΠΩΝ ΤΟΥ ΕΡΓΟΥ.
3. ΟΙ ΔΙΑΣΤΑΣΕΙΣ ΤΩΝ ΚΟΥΟΝΕΝΟΜΑΤΩΝ ΣΤΑ ΑΡΧΙΤΕΚΤΟΝΙΚΑ ΕΙΝΑΙ ΚΑΘΑΡΕΣ. Ο ΕΡΓΟΛΑΒΟΣ ΕΙΝΑΙ ΥΠΟΧΡΕΩΣ ΝΑ ΚΑΤΑΣΚΕΥΑΣΗ ΤΑ ΚΟΥΟΝΕΝΩΜΑΤΑ ΛΑΜΒΑΝΟΝΤΑΣ ΥΠΟΦ.Η 3 ΧΕΡΙΑ ΣΟΥΒΑ ΚΑΙ ΠΟΛΥΣΤΕΡΙΝΗ ΚΑΙ ΟΠΟΙΟΔΗΠΟΤΕ ΤΕΛΙΚΟ ΕΠΙΧΡΙΣΜΑ.

D.W = ΠΛΥΝΤΗΡΙΟ ΠΙΑΤΩΝ
W.M = ΠΛΥΝΤΗΡΙΟ ΡΟΥΧΩΝ
Σ.Ρ = ΣΤΕΓΝΩΤΗΡΙΟ ΡΟΥΧΩΝ
F.. = Φ.ΥΓΕΙΟ
OVEN. = ΟΒΕΝΟΥΡΝΟΣ

BY :	DATE :	REVISION :
-	-	-
-	-	-
-	-	-
-	-	-
-	-	-
-	-	-
-	-	-
-	-	-
-	-	-

EL = EXISTING LEVEL
YOVENISTAMENO YF.OMETPO
ERL = EXISTING ROAD LEVEL
YOVENISTAMENO YF.OMETPO ΔΡΟΜΟΥ
EPL = EXISTING PAVEMENT LEVEL
YOVENISTAMENO YF.OMETPO ΠΕΖΟΔΡΟΜΙΟΥ

PGL = PROPOSED GROUND LEVEL
ΠΡΟΤΕΙΝΟΜΕΝΟ ΥΦ.ΟΜΕΤΡΟ ΕΔΑΦΟΝΟΥΣ
FFL = FINISHED FLOOR LEVEL
ΥΦ.ΟΜΕΤΡΟ ΤΕΛΕΙΩΜΕΝΟΥ ΠΙΑΤΟΜΑΤΟΣ
SSL = STRUCTURAL SLAB LEVEL
ΔΟΜΙΚΟ ΥΦ.ΟΜΕΤΡΟ ΠΛΑΚΑΣ
TOB = TOP OF BEAM
ΔΟΜΙΚΟ ΥΦ.ΟΜΕΤΡΟ ΠΛΑΤΗ ΜΕΡΟΥΣ ΔΟΚΟΥ
TOP = TOP OF PARAPET
ΔΟΜΙΚΟ ΥΦ.ΟΜΕΤΡΟ ΠΛΑΤΗ ΜΕΡΟΥΣ ΣΤΗΘΑΙΟΥ

CODE ARCHITECTURE STUDIO
ARCHITECTS & ENGINEERS

MICHALIS NEOFYTOU
ARCHITECT N.T.U.A.-MA ARCHITECTURE

ΜΙΧΑΗΛΗΣ ΝΕΟΦΥΤΟΥ
ΑΡΧΙΤΕΚΤΟΝΑΣ
EMP - MA ARCHITECTURE
A.M.: A116407

ΑΓΙΟΥ ΑΝΤΩΝΙΟΥ 6
NIKA TOWER FLAT 202
7102, ARADIPPOY
LARNACA-CYPRUS
TEL. 24534204 FAX. 24323019
EMAIL INFO@CA-STUDIO.COM

JOB TITLE : ΠΟΛΥΚΑΤΟΙΚΙΑ 12 ΔΙΑΜΕΡΙΣΜΑΤΩΝ

OWNER : DEXTEK CONTRACTORS LIMITED

SHEET TITLE : ΚΑΤΟΨΗ 1ΟΥ ΟΡΟΦΟΥ


DATE : ΔΕΚΕΜΒΡΙΟΣ 2024

A 03

SCALE : 1 : 100 @ A3

DESIGN
T.R

JOB NO
594

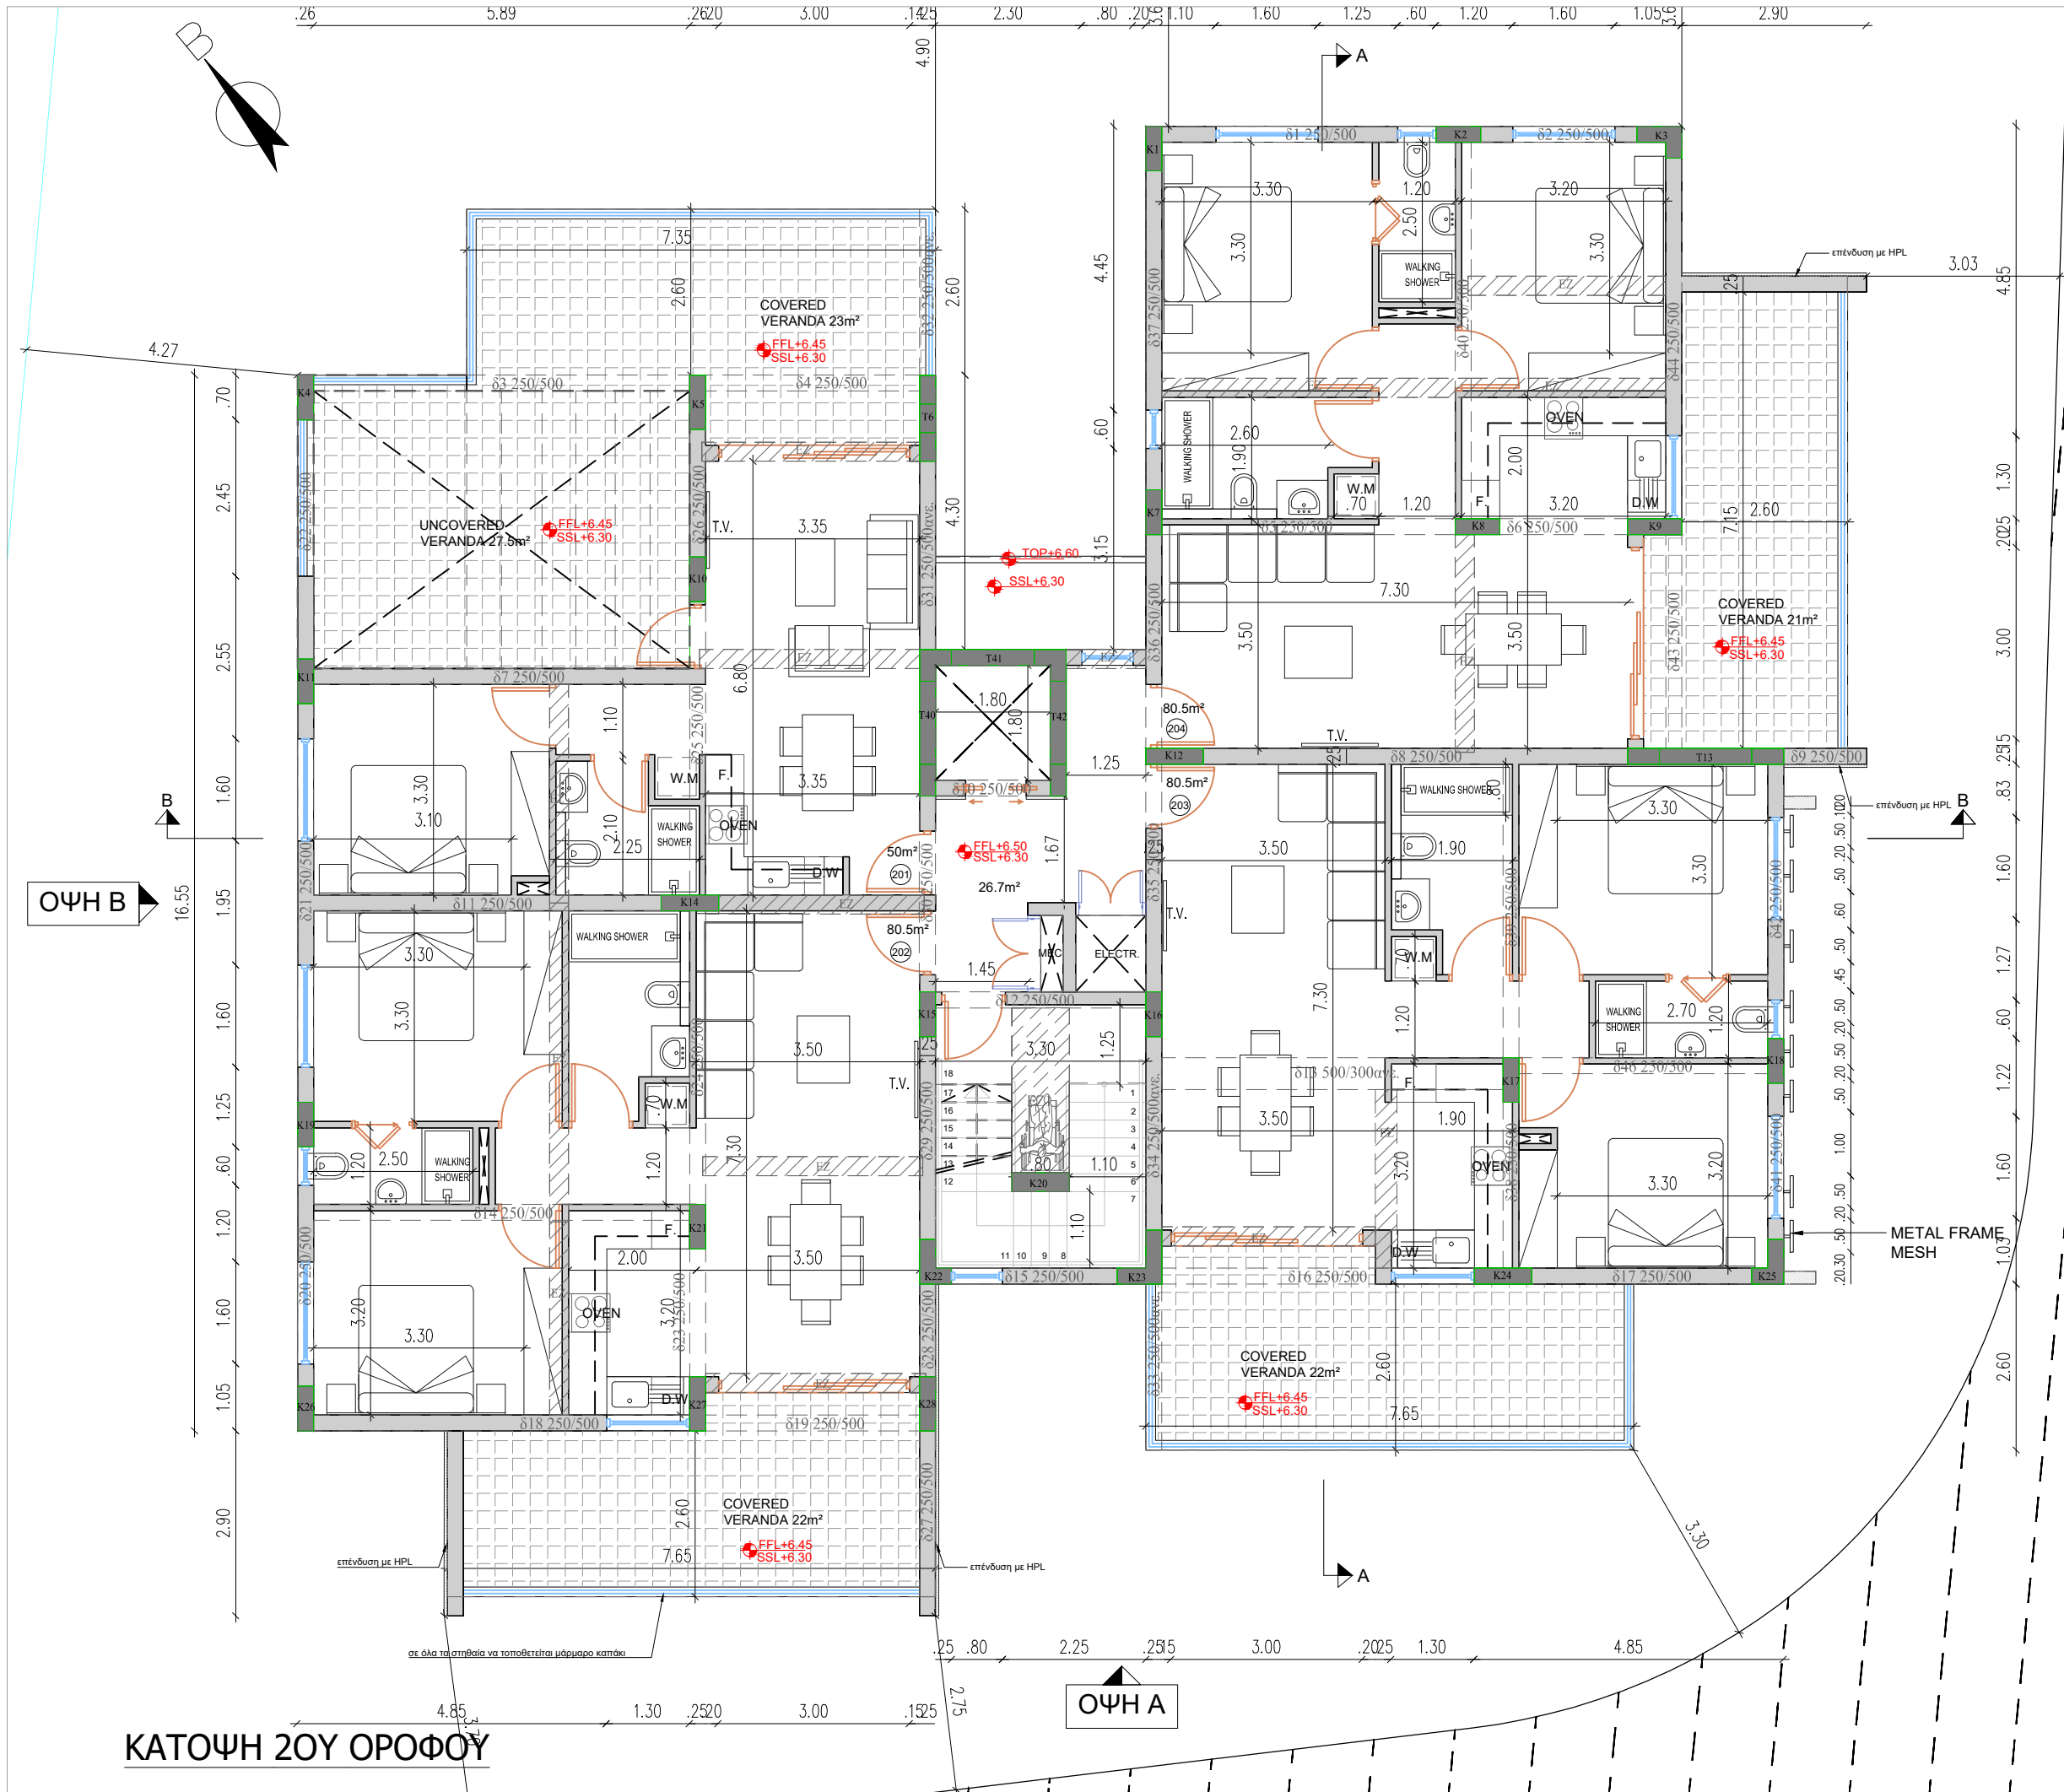

NOTES :

1. ΟΛΑ ΤΑ ΥΛΙΚΑ ΝΑ ΧΡΗΣΙΜΟΠΟΙΗΘΟΥΝ ΜΕ ΤΗ ΣΥΓΚΑΤΑΘΕΣΗ ΤΟΥ ΑΡΧΙΤΕΚΤΟΝΑ.
2. ΟΛΑ ΤΑ ΑΡΧΙΤΕΚΤΟΝΙΚΑ ΣΧΕΔΙΑ ΚΑΙ ΛΕΠΤΟΜΕΡΕΙΕΣ ΝΑ ΔΙΑΒΑΖΟΝΤΑΙ ΜΑΖΙ ΜΕ ΤΑ ΣΤΑΤΙΚΑ & ΗΛΕΚΤΡΟΜΗΧΑΝΟΛΟΓΙΚΑ ΣΧΕΔΙΑ. ΓΙΑ ΟΠΟΙΕΣΔΗΠΟΤΕ ΔΙΑΦΟΡΕΣ ΝΑ ΕΝΗΜΕΡΩΝΕΤΑΙ Ο ΕΠΙΒΛΕΠΩΝ ΤΟΥ ΕΡΓΟΥ.
3. ΟΙ ΔΙΑΣΤΑΣΕΙΣ ΤΩΝ ΚΟΥΟΝΕΝΟΜΑΤΩΝ ΣΤΑ ΑΡΧΙΤΕΚΤΟΝΙΚΑ ΕΙΝΑΙ ΚΑΘΑΡΕΣ. Ο ΕΡΓΟΛΑΒΟΣ ΕΙΝΑΙ ΥΠΟΧΡΕΩΣ ΝΑ ΚΑΤΑΣΚΕΥΑΣΗ ΤΑ ΚΟΥΟΝΕΝΩΜΑΤΑ ΛΑΜΒΑΝΟΝΤΑΣ ΥΠΟΦ.Η 3 ΧΕΡΙΑ ΣΟΥΒΑ ΚΑΙ ΠΟΛΥΣΤΕΡΙΝΗ ΚΑΙ ΟΠΟΙΟΔΗΠΟΤΕ ΤΕΛΙΚΟ ΕΠΙΧΡΙΣΜΑ.

D.W = ΠΛΥΝΤΗΡΙΟ ΠΙΑΤΩΝ
W.M = ΠΛΥΝΤΗΡΙΟ ΡΟΥΧΩΝ
Σ.Ρ = ΣΤΕΓΝΩΤΗΡΙΟ ΡΟΥΧΩΝ
F.. = Φ.ΥΓΕΙΟ
OVEN. = ΟΒΕΝΟΥΡΝΟΣ

BY :	DATE :	REVISION :
-	-	-
-	-	-
-	-	-
-	-	-
-	-	-
-	-	-
-	-	-
-	-	-
-	-	-

EL = EXISTING LEVEL
YOVENISTAMENO YF.OMETPO
ERL = EXISTING ROAD LEVEL
YOVENISTAMENO YF.OMETPO ΔΡΟΜΟΥ
EPL = EXISTING PAVEMENT LEVEL
YOVENISTAMENO YF.OMETPO ΠΕΖΟΔΡΟΜΙΟΥ

PGL = PROPOSED GROUND LEVEL
ΠΡΟΤΕΙΝΟΜΕΝΟ YF.OMETPO ΕΔΑΦΟΕΝΟΥΣ
FFL = FINISHED FLOOR LEVEL
YF.OMETPO ΤΕΛΕΙΩΜΕΝΟΥ ΠΑΤΩΜΑΤΟΣ
SSL = STRUCTURAL SLAB LEVEL
ΔΟΜΙΚΟ YF.OMETPO ΠΛΑΚΑΣ
TOB = TOP OF BEAM
ΔΟΜΙΚΟ YF.OMETPO ΠΛΑΤΗ ΜΕΡΟΥΣ ΔΟΚΟΥ
TOP = TOP OF PARAPET
ΔΟΜΙΚΟ YF.OMETPO ΠΛΑΤΗ ΜΕΡΟΥΣ ΣΤΗΘΑΙΟΥ

CODE ARCHITECTURE STUDIO
ARCHITECTS & ENGINEERS

MICHALIS NEOFYTOU
ARCHITECT N.T.U.A.-MA ARCHITECTURE

ΜΙΧΑΛΗΣ ΝΕΟΦΥΤΟΥ
ΑΡΧΙΤΕΚΤΟΝΑΣ
EMP - MA ARCHITECTURE
A.M.: A116407

ΑΓΙΟΥ ΑΝΤΩΝΙΟΥ 6
NIKA TOWER FLAT 202
7102, ARADIPPOY
LARNACA-CYPRUS
TEL. 24534204 FAX. 24323019
EMAIL INFO@CA-STUDIO.COM

JOB TITLE : ΠΟΛΥΚΑΤΟΙΚΙΑ 12 ΔΙΑΜΕΡΙΣΜΑΤΩΝ

OWNER : DEXTEK CONTRACTORS LIMITED

SHEET TITLE : ΚΑΤΟΨΗ 2ΟΥ ΟΡΟΦΟΥ


DATE : ΔΕΚΕΜΒΡΙΟΣ 2024

A 04

SCALE : 1 : 100 @ A3

DESIGN
T.R

JOB NO
594

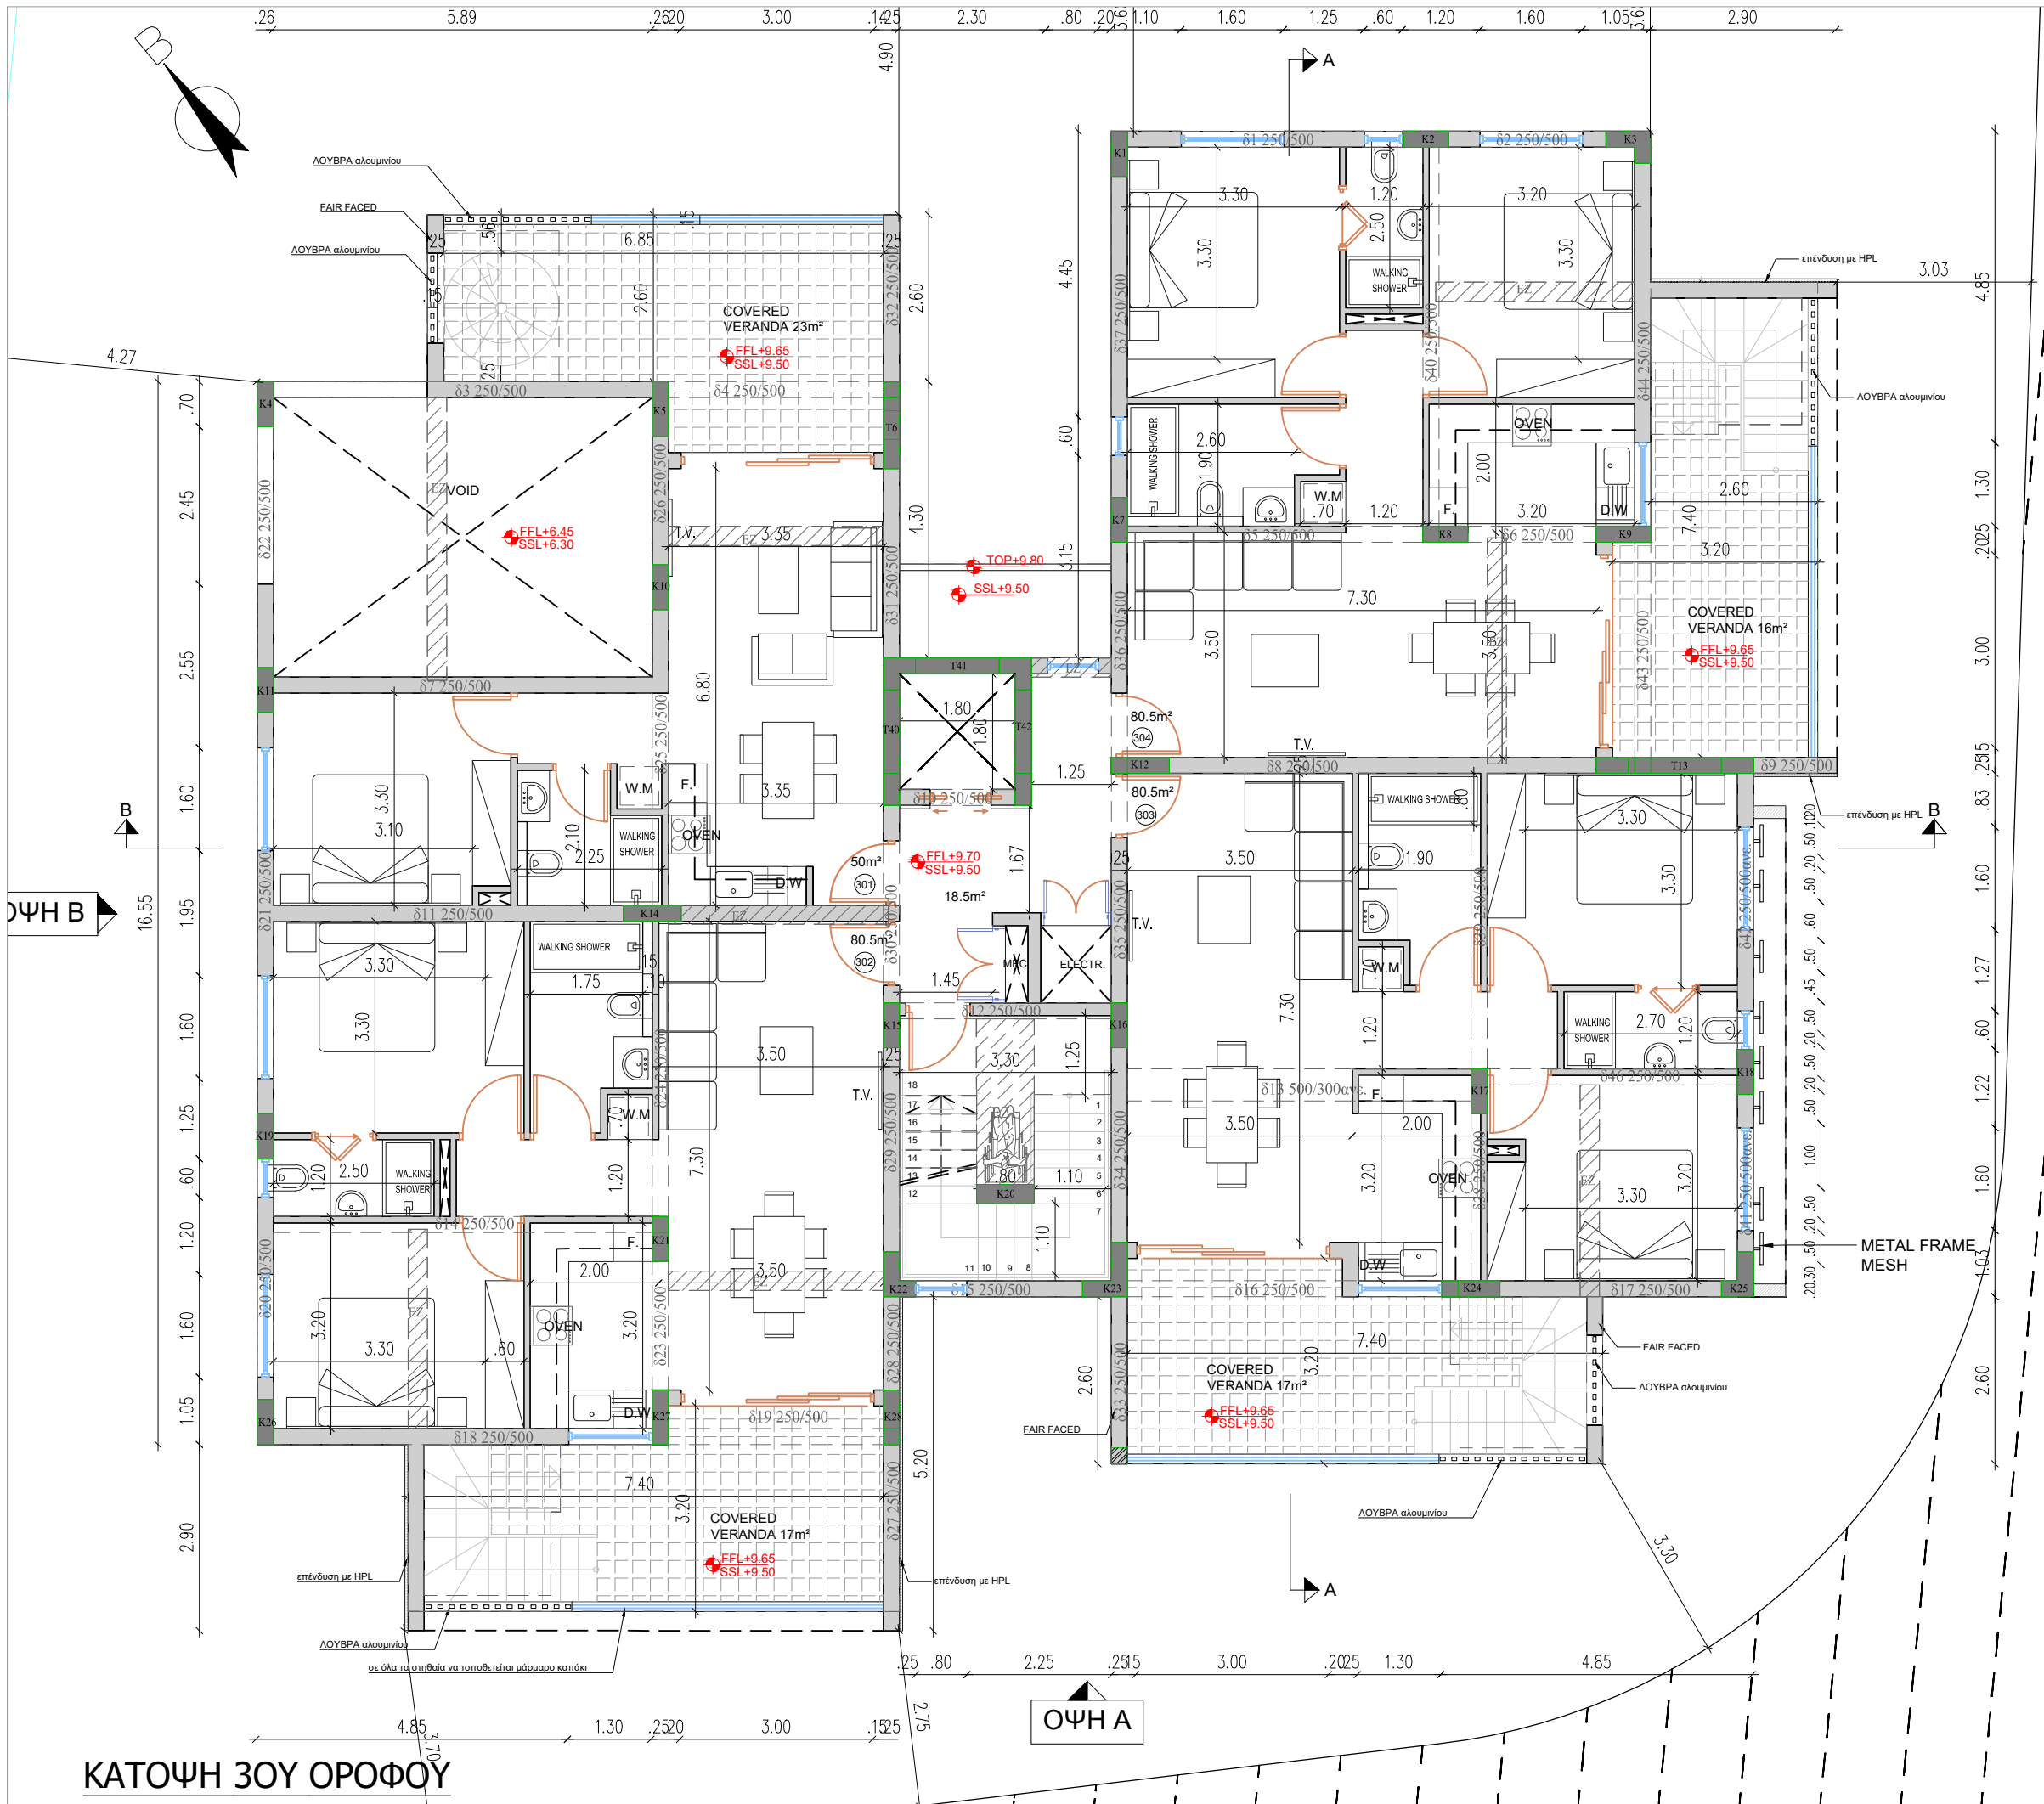

NOTES :

1. ΟΛΑ ΤΑ ΥΛΙΚΑ ΝΑ ΧΡΗΣΙΜΟΠΟΙΗΘΟΥΝ ΜΕ ΤΗ ΣΥΓΚΑΤΑΘΕΣΗ ΤΟΥ ΑΡΧΙΤΕΚΤΟΝΑ.
2. ΟΛΑ ΤΑ ΑΡΧΙΤΕΚΤΟΝΙΚΑ ΣΧΕΔΙΑ ΚΑΙ ΛΕΠΤΟΜΕΡΕΙΕΣ ΝΑ ΔΙΑΒΑΖΟΝΤΑΙ ΜΑΖΙ ΜΕ ΤΑ ΣΤΑΤΙΚΑ & ΗΛΕΚΤΡΟΜΗΧΑΝΟΛΟΓΙΚΑ ΣΧΕΔΙΑ. ΓΙΑ ΟΠΟΙΕΣΔΗΠΟΤΕ ΔΙΑΦΟΡΕΣ ΝΑ ΕΝΗΜΕΡΩΝΕΤΑΙ Ο ΕΠΙΒΛΕΠΩΝ ΤΟΥ ΕΡΓΟΥ.
3. ΟΙ ΔΙΑΣΤΑΣΕΙΣ ΤΩΝ ΚΟΥΟΝΕΝΟΜΑΤΩΝ ΣΤΑ ΑΡΧΙΤΕΚΤΟΝΙΚΑ ΕΙΝΑΙ ΚΑΘΑΡΕΣ. Ο ΕΡΓΟΛΑΒΟΣ ΕΙΝΑΙ ΥΠΟΧΡΕΩΣ ΝΑ ΚΑΤΑΣΚΕΥΑΣΗ ΤΑ ΚΟΥΟΝΕΝΩΜΑΤΑ ΛΑΜΒΑΝΟΝΤΑΣ ΥΠΟΨΗ 3 ΧΕΡΙΑ ΣΟΥΒΑ ΚΑΙ ΠΟΛΥΣΤΕΡΙΝΗ ΚΑΙ ΟΠΟΙΟΔΗΠΟΤΕ ΤΕΛΙΚΟ ΕΠΙΧΡΙΣΜΑ.

D.W = ΠΛΥΝΤΗΡΙΟ ΠΙΑΤΩΝ
W.M = ΠΛΥΝΤΗΡΙΟ ΡΟΥΧΩΝ
Σ.Ρ = ΣΤΕΓΝΩΤΗΡΙΟ ΡΟΥΧΩΝ
F.. = Φ.ΥΓΕΙΟ
OVEN. = ΟΒΕΝΟΥΡΝΟΣ

BY :	DATE :	REVISION :
-	-	-
-	-	-
-	-	-
-	-	-
-	-	-
-	-	-
-	-	-
-	-	-
-	-	-

EL = EXISTING LEVEL
YOYENISTAMENO YF.OMETPO
ERL = EXISTING ROAD LEVEL
YOYENISTAMENO YF.OMETPO ΔΡΟΜΟΥ
EPL = EXISTING PAVEMENT LEVEL
YOYENISTAMENO YF.OMETPO ΠΕΖΟΔΡΟΜΙΟΥ

PGL = PROPOSED GROUND LEVEL
ΠΡΟΤΕΙΝΟΜΕΝΟ ΥΦ.ΟΜΕΤΡΟ ΕΔΑΦΟΕΝΟΥΣ
FFL = FINISHED FLOOR LEVEL
ΥΦ.ΟΜΕΤΡΟ ΤΕΛΕΙΩΜΕΝΟΥ ΠΑΤΩΜΑΤΟΣ
SSL = STRUCTURAL SLAB LEVEL
ΔΟΜΙΚΟ ΥΦ.ΟΜΕΤΡΟ ΠΛΑΚΑΣ
TOB = TOP OF BEAM
ΔΟΜΙΚΟ ΥΦ.ΟΜΕΤΡΟ ΠΛΑΝΟ ΜΕΡΟΥΣ ΔΟΚΟΥ
TOP = TOP OF PARAPET
ΔΟΜΙΚΟ ΥΦ.ΟΜΕΤΡΟ ΠΛΑΝΟ ΜΕΡΟΥΣ ΣΤΗΘΑΙΟΥ

CODE ARCHITECTURE STUDIO
ARCHITECTS & ENGINEERS

MICHALIS NEOFYTOU
ARCHITECT N.T.U.A.-MA ARCHITECTURE

ΜΙΧΑΛΗΣ ΝΕΟΦΥΤΟΥ
ΑΡΧΙΤΕΚΤΟΝΑΣ
EMP-MA ARCHITECTURE
A.M.: A116407

ΑΓΙΟΥ ΑΝΤΩΝΙΟΥ 6
NIKA TOWER FLAT 202
7102, ARADIPPOY
LARNACA-CYPRUS
TEL. 24534204 FAX. 24323019
EMAIL INFO@CA-STUDIO.COM

JOB TITLE : ΠΟΛΥΚΑΤΟΙΚΙΑ 12 ΔΙΑΜΕΡΙΣΜΑΤΩΝ

OWNER : DEXTEK CONTRACTORS LIMITED

SHEET TITLE : ΚΑΤΟΨΗ 3ΟΥ ΟΡΟΦΟΥ


DATE : ΔΕΚΕΜΒΡΙΟΣ 2024

A 05


SCALE : 1 : 100 @ A3

DESIGN
T.R

JOB NO
594

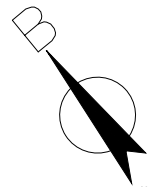

σε όλα τα σημεία να τοποθετείται μάρμαρο κατάκτι

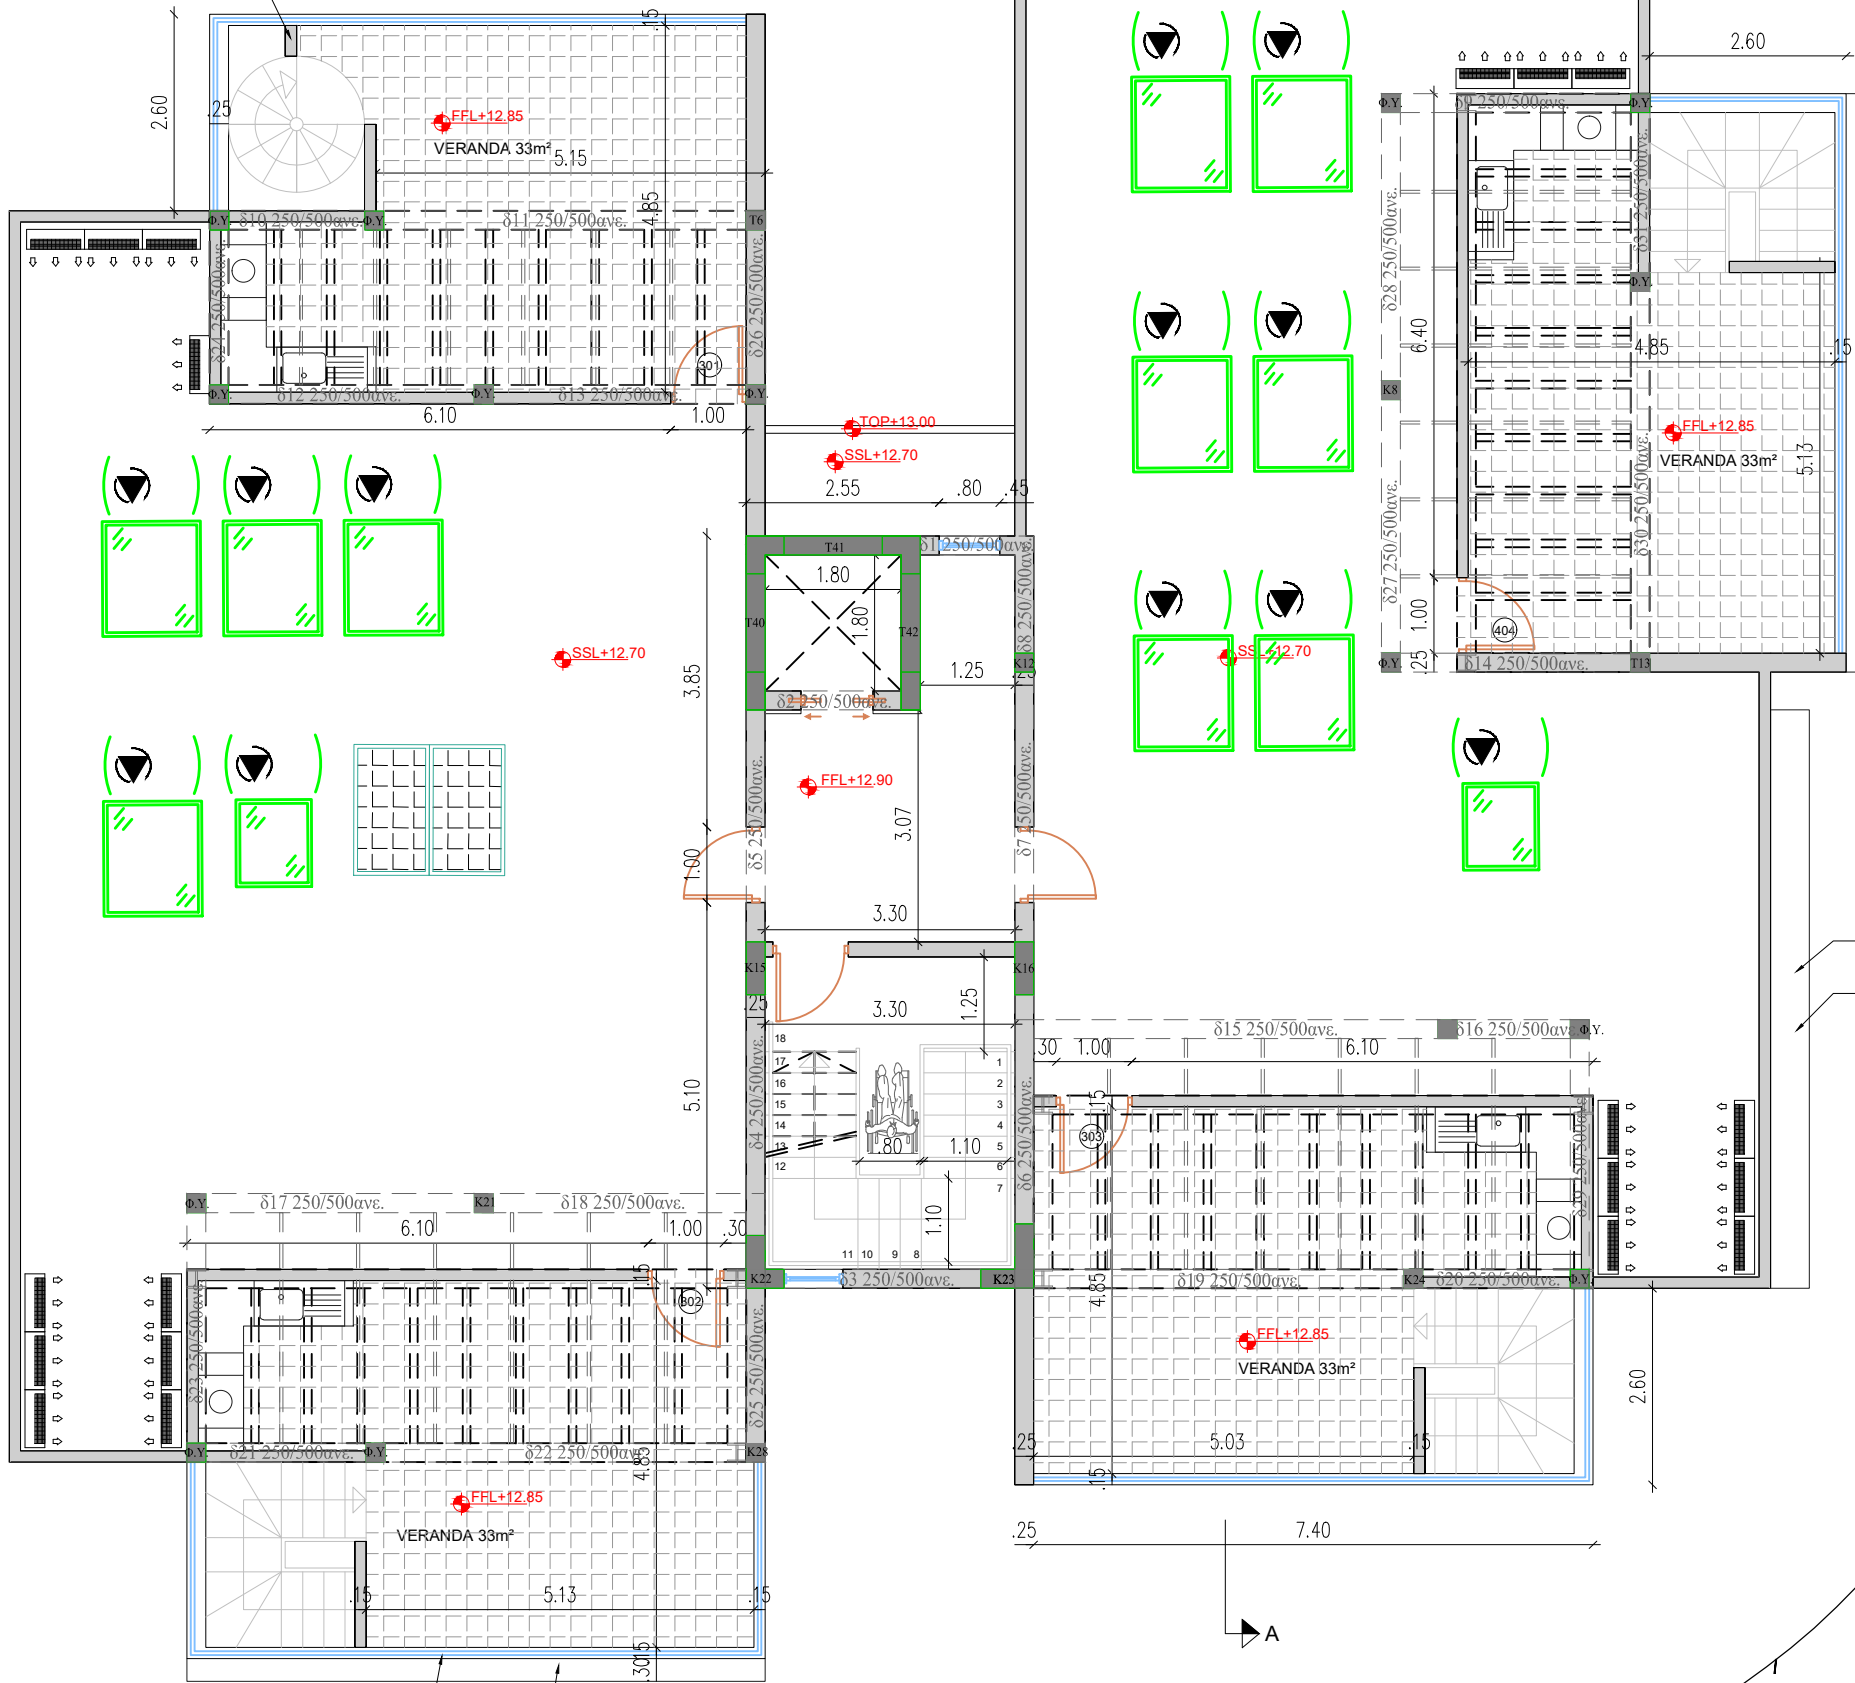

ΚΑΤΟΨΗ ROOF GARDEN

ΟΨΗ Α

NOTES :

1. ΟΛΑ ΤΑ ΥΛΙΚΑ ΝΑ ΧΡΗΣΙΜΟΠΟΙΗΘΟΥΝ ΜΕ ΤΗ ΣΥΓΚΑΤΑΘΕΣΗ ΤΟΥ ΑΡΧΙΤΕΚΤΟΝΑ.

2. ΟΛΑ ΤΑ ΑΡΧΙΤΕΚΤΟΝΙΚΑ ΣΧΕΔΙΑ ΚΑΙ ΛΕΠΤΟΜΕΡΕΙΕΣ ΝΑ ΔΙΑΒΑΖΟΝΤΑΙ ΜΑΖΙ ΜΕ ΤΑ ΣΤΑΤΙΚΑ & ΗΛΕΚΤΡΟΜΗΧΑΝΟΛΟΓΙΚΑ ΣΧΕΔΙΑ. ΓΙΑ ΟΠΟΙΕΣΔΗΠΟΤΕ ΔΙΑΦΕΡΟΝΤΕΣ ΝΑ ΕΝΗΜΕΡΩΝΕΤΑΙ Ο ΕΠΙΒΛΕΠΩΝ ΤΟΥ ΕΡΓΟΥ.

3. ΟΙ ΔΙΑΣΤΑΣΕΙΣ ΤΩΝ ΚΟΥΟΝΕΝΟΜΑΤΩΝ ΣΤΑ ΑΡΧΙΤΕΚΤΟΝΙΚΑ ΕΙΝΑΙ ΚΑΘΑΡΕΣ. Ο ΕΡΓΟΛΑΒΟΣ ΕΙΝΑΙ ΥΠΟΧΡΕΩΣ ΝΑ ΚΑΤΑΣΚΕΥΑΣΗ ΤΑ ΚΟΥΟΝΕΝΩΜΑΤΑ ΛΑΜΒΑΝΟΝΤΑΣ ΥΠΟΦ.Η 3 ΧΕΡΙΑ ΣΟΥΒΑ ΚΑΙ ΠΟΛΥΣΤΕΡΙΝΗ ΚΑΙ ΟΠΟΙΟΔΗΠΟΤΕ ΤΕΛΙΚΟ ΕΠΙΧΡΙΣΜΑ.

D.W = ΠΛΥΝΤΗΡΙΟ ΠΙΑΤΩΝ
W.M = ΠΛΥΝΤΗΡΙΟ ΡΟΥΧΩΝ
Σ.Ρ = ΣΤΕΓΝΩΤΗΡΙΟ ΡΟΥΧΩΝ
F.. = F.ΥΓΕΙΟ
OVEN. = ΟΥΕΝΟΥΡΝΟΣ

BY :	DATE :	REVISION :
-	-	-
-	-	-
-	-	-
-	-	-
-	-	-
-	-	-
-	-	-
-	-	-
-	-	-
-	-	-
-	-	-

EL = EXISTING LEVEL ΥΦΟΝΙΣΤΑΜΕΝΟ ΥΦ.ΟΜΕΤΡΟ	PGL = PROPOSED GROUND LEVEL ΠΡΟΤΕΙΝΟΜΕΝΟ ΥΦ.ΟΜΕΤΡΟ ΕΔΑΦΟΥΣ
ERL = EXISTING ROAD LEVEL	FFL = FINISHED FLOOR LEVEL ΥΦ.ΟΜΕΤΡΟ ΤΕΛΕΙΩΜΕΝΟΥ ΠΑΤΩΜΑΤΟΣ
YOVENISTAMENO YF.OMETRO APOMOIY EPL = EXISTING PAVEMENT LEVEL	SSL = STRUCTURAL SLAB LEVEL ΔΟΜΙΚΟ ΥΦ.ΟΜΕΤΡΟ ΠΛΑΚΑΣ
YOVENISTAMENO YF.OMETRO PEZODROMOIY	DOB = TOP OF BEAM ΔΟΜΙΚΟ ΥΦ.ΟΜΕΤΡΟ ΠΛΑΤΩ ΜΕΡΟΥΣ ΔΟΚΟΥ
	TOP = TOP OF PARAPET ΔΟΜΙΚΟ ΥΦ.ΟΜΕΤΡΟ ΠΛΑΤΩ ΜΕΡΟΥΣ ΣΤΗΘΑΙΟΥ

CODE ARCHITECTURE STUDIO
ARCHITECTS & ENGINEERS

MICHALIS NEOFYTOY
ARCHITECT N.T.U.A.-MA ARCHITECTURE

ΜΙΧΑΛΗΣ ΝΕΟΦΥΤΟΥ
ΑΡΧΙΤΕΚΤΟΝΑΣ
EMP - MA ARCHITECTURE
A.M.: A116407

ΑΓΙΟΥ ΑΝΤΩΝΙΟΥ 6
NIKA TOWER FLAT 202
7102, ARADIPPOY
LARNACA-CYPRUS
TEL. 24534204 FAX. 24323019
EMAIL INFO@CA-STUDIO.COM

JOB TITLE : ΠΟΛΥΚΑΤΟΙΚΙΑ 12 ΔΙΑΜΕΡΙΣΜΑΤΩΝ

OWNER : DEXTEK CONTRACTORS LIMITED

SHEET TITLE : ΚΑΤΟΨΗ ROOF GARDEN

DATE : ΔΕΚΕΜΒΡΙΟΣ 2024

A 06

SCALE : 1 : 100 @ A3

DESIGN	JOB NO
T.R	594



ΟΨΗ Α

NOTES :

1. ΟΛΑ ΤΑ ΥΛΙΚΑ ΝΑ ΧΡΗΣΙΜΟΠΟΙΗΘΟΥΝ ΜΕ ΤΗ ΣΥΓΚΑΤΑΘΕΣΗ ΤΟΥ ΑΡΧΙΤΕΚΤΟΝΑ.

2. ΟΛΑ ΤΑ ΑΡΧΙΤΕΚΤΟΝΙΚΑ ΣΧΕΔΙΑ ΚΑΙ ΛΕΠΤΟΜΕΡΕΙΕΣ ΝΑ ΔΙΑΒΑΖΟΝΤΑΙ ΜΑΖΙ ΜΕ ΤΑ ΣΤΑΤΙΚΑ & ΗΛΕΚΤΡΟΜΗΧΑΝΟΛΟΓΙΚΑ ΣΧΕΔΙΑ. ΓΙΑ ΟΠΟΙΕΣΔΗΠΟΤΕ ΔΙΑΦΟΡΕΣ ΝΑ ΕΝΗΜΕΡΩΝΕΤΑΙ Ο ΕΠΙΒΛΕΠΩΝ ΤΟΥ ΕΡΓΟΥ.

3. ΟΙ ΔΙΑΣΤΑΣΕΙΣ ΤΩΝ ΚΟΥΟΝΕΝΟΜΑΤΩΝ ΣΤΑ ΑΡΧΙΤΕΚΤΟΝΙΚΑ ΕΙΝΑΙ ΚΑΘΑΡΕΣ. Ο ΕΡΓΟΛΑΒΟΣ ΕΙΝΑΙ ΥΠΟΧΡΕΟΣ ΝΑ ΚΑΤΑΣΚΕΥΑΣΗ ΤΑ ΚΟΥΟΝΕΝΩΜΑΤΑ ΛΑΜΒΑΝΟΝΤΑΣ ΥΠΟΨΗ 3 ΧΕΡΙΑ ΣΟΥΒΑ ΚΑΙ ΠΟΛΥΣΤΕΡΙΝΗ ΚΑΙ ΟΠΟΙΟΔΗΠΟΤΕ ΤΕΛΙΚΟ ΕΠΙΧΡΙΣΜΑ.

D.W = ΠΛΥΝΤΗΡΙΟ ΠΙΑΤΩΝ
W.M = ΠΛΥΝΤΗΡΙΟ ΡΟΥΧΩΝ
Σ.Ρ = ΣΤΕΓΝΩΤΗΡΙΟ ΡΟΥΧΩΝ
F.. = Φ.ΥΓΕΙΟ
OVEN. = ΟΥΕΝΟΥΡΝΟΣ

BY :	DATE :	REVISION :
-	-	-
-	-	-
-	-	-
-	-	-
-	-	-
-	-	-
-	-	-
-	-	-
-	-	-

EL = EXISTING LEVEL
ΥΦΙΣΤΑΜΕΝΟ ΥΨ.ΟΜΕΤΡΟ

ERL = EXISTING ROAD LEVEL
ΥΦΙΣΤΑΜΕΝΟ ΥΨ.ΟΜΕΤΡΟ ΔΡΟΜΟΥ

EPL = EXISTING PAVEMENT LEVEL
ΥΦΙΣΤΑΜΕΝΟ ΥΨ.ΟΜΕΤΡΟ ΠΕΖΟΔΡΟΜΙΟΥ

PGL = PROPOSED GROUND LEVEL
ΠΡΟΤΕΙΝΟΜΕΝΟ ΥΨ.ΟΜΕΤΡΟ ΕΔΑΦΟΕΝΟΥΣ

FFL = FINISHED FLOOR LEVEL
ΥΨ.ΟΜΕΤΡΟ ΤΕΛΕΙΩΜΕΝΟΥ ΠΙΑΤΩΜΑΤΟΣ

SSL = STRUCTURAL SLAB LEVEL
ΔΟΜΙΚΟ ΥΨ.ΟΜΕΤΡΟ ΠΛΑΚΑΣ

TOB = TOP OF BEAM
ΔΟΜΙΚΟ ΥΨ.ΟΜΕΤΡΟ ΠΛΑΤΩ ΜΕΡΟΥΣ ΔΟΚΟΥ

TOP = TOP OF PARAPET
ΔΟΜΙΚΟ ΥΨ.ΟΜΕΤΡΟ ΠΛΑΤΩ ΜΕΡΟΥΣ ΣΤΗΘΑΙΟΥ

CODE ARCHITECTURE STUDIO
ARCHITECTS & ENGINEERS

MICHALIS NEOFYTOU
ARCHITECT N.T.U.A.-MA ARCHITECTURE

ΜΙΧΑΛΗΣ ΝΕΟΦΥΤΟΥ
ΑΡΧΙΤΕΚΤΟΝΑΣ
EMP - MA ARCHITECTURE
A.M.: A116407

ΑΓΙΟΥ ΑΝΤΩΝΙΟΥ 6
ΝΙΚΑ ΤOWER FLAT 202
7102, ΑΡΑΔΙΠΠΟΥ
ΛΑΡΝΑΚΑ-ΚΥΠΡΟΣ
TEL. 24534204 FAX. 24323019
EMAIL INFO@CA-STUDIO.COM

JOB TITLE : ΠΟΛΥΚΑΤΟΙΚΙΑ 12 ΔΙΑΜΕΡΙΣΜΑΤΩΝ

OWNER : DEXTEK CONTRACTORS LIMITED

SHEET TITLE : ΟΨΗ Α

DATE : ΔΕΚΕΜΒΡΙΟΣ 2024	A 08
SCALE : 1 : 100 @ A3	DESIGN T.R. JOB NO 594



ΟΨΗ Β

NOTES :

1. ΟΛΑ ΤΑ ΥΛΙΚΑ ΝΑ ΧΡΗΣΙΜΟΠΟΙΗΘΟΥΝ ΜΕ ΤΗ ΣΥΓΚΑΤΑΘΕΣΗ ΤΟΥ ΑΡΧΙΤΕΚΤΟΝΑ.
2. ΟΛΑ ΤΑ ΑΡΧΙΤΕΚΤΟΝΙΚΑ ΣΧΕΔΙΑ ΚΑΙ ΛΕΠΤΟΜΕΡΕΙΕΣ ΝΑ ΔΙΑΒΑΖΟΝΤΑΙ ΜΑΖΙ ΜΕ ΤΑ ΣΤΑΤΙΚΑ & ΗΛΕΚΤΡΟΜΗΧΑΝΟΛΟΓΙΚΑ ΣΧΕΔΙΑ. ΓΙΑ ΟΠΟΙΕΣΔΗΠΟΤΕ ΔΙΑΦΟΡΕΣ ΝΑ ΕΝΗΜΕΡΩΝΕΤΑΙ Ο ΕΠΙΒΛΕΠΩΝ ΤΟΥ ΕΡΓΟΥ.
3. ΟΙ ΔΙΑΣΤΑΣΕΙΣ ΤΩΝ ΚΟΥΟΝΕΝΟΜΑΤΩΝ ΣΤΑ ΑΡΧΙΤΕΚΤΟΝΙΚΑ ΕΙΝΑΙ ΚΑΘΑΡΕΣ. Ο ΕΡΓΟΛΑΒΟΣ ΕΙΝΑΙ ΥΠΟΧΡΕΟΣ ΝΑ ΚΑΤΑΣΚΕΥΑΣΗ ΤΑ ΚΟΥΟΝΕΝΩΜΑΤΑ ΛΑΜΒΑΝΟΝΤΑΣ ΥΠΟΨΗ 3 ΧΕΡΙΑ ΣΟΥΒΑ ΚΑΙ ΠΟΛΥΣΤΕΡΙΝΗ ΚΑΙ ΟΠΟΙΟΔΗΠΟΤΕ ΤΕΛΙΚΟ ΕΠΙΧΡΙΣΜΑ.
- D.W = ΠΛΥΝΤΗΡΙΟ ΠΙΑΤΩΝ
W.M = ΠΛΥΝΤΗΡΙΟ ΡΟΥΧΩΝ
Σ.Ρ = ΣΤΕΓΝΩΤΗΡΙΟ ΡΟΥΧΩΝ
F.. = Φ.ΥΓΕΙΟ
OVEN. = ΟΥΕΝΟΥΡΝΟΣ

BY :	DATE :	REVISION :
-	-	-
-	-	-
-	-	-
-	-	-
-	-	-
-	-	-
-	-	-
-	-	-
-	-	-

- EL = EXISTING LEVEL
ΥΦΟΝΙΣΤΑΜΕΝΟ ΥΨ.ΟΜΕΤΡΟ
ERL = EXISTING ROAD LEVEL
ΥΦΟΝΙΣΤΑΜΕΝΟ ΥΨ.ΟΜΕΤΡΟ ΔΡΟΜΟΥ
EPL = EXISTING PAVEMENT LEVEL
ΥΦΟΝΙΣΤΑΜΕΝΟ ΥΨ.ΟΜΕΤΡΟ ΠΕΖΟΔΡΟΜΙΟΥ
- PGL = PROPOSED GROUND LEVEL
ΠΡΟΤΕΙΝΟΜΕΝΟ ΥΨ.ΟΜΕΤΡΟ ΕΔΑΦΟΥΣ
FFL = FINISHED FLOOR LEVEL
ΥΨ.ΟΜΕΤΡΟ ΤΕΛΕΙΩΜΕΝΟΥ ΠΙΑΤΩΜΑΤΟΣ
SSL = STRUCTURAL SLAB LEVEL
ΔΟΜΙΚΟ ΥΨ.ΟΜΕΤΡΟ ΠΛΑΚΑΣ
TOB = TOP OF BEAM
ΔΟΜΙΚΟ ΥΨ.ΟΜΕΤΡΟ ΠΛΑΤΩ ΜΕΡΟΥΣ ΔΟΚΟΥ
TOP = TOP OF PARAPET
ΔΟΜΙΚΟ ΥΨ.ΟΜΕΤΡΟ ΠΛΑΤΩ ΜΕΡΟΥΣ ΣΤΗΘΑΙΟΥ

CODE ARCHITECTURE STUDIO
ARCHITECTS & ENGINEERS

MICHALIS NEOFYTOU
ARCHITECT N.T.U.A.-MA ARCHITECTURE

ΜΙΧΑΛΗΣ ΝΕΟΦΥΤΟΥ
ΑΡΧΙΤΕΚΤΟΝΑΣ
EMP - MA ARCHITECTURE
A.M.: A116407

ΑΓΙΟΥ ΑΝΤΩΝΙΟΥ 6
NIKA TOWER FLAT 202
7102, ARADIPPOY
LARNACA-CYPRUS
TEL. 24534204 FAX. 24323019
EMAIL INFO@CA-STUDIO.COM

JOB TITLE : ΠΟΛΥΚΑΤΟΙΚΙΑ 12 ΔΙΑΜΕΡΙΣΜΑΤΩΝ

OWNER : DEXTEK CONTRACTORS LIMITED

SHEET TITLE : ΟΨΗ Β

DATE : ΔΕΚΕΜΒΡΙΟΣ 2024

A 09

SCALE : 1 : 100 @ A3

DESIGN
T.R

JOB NO
594



ΟΨΗ Γ

NOTES :

1. ΟΛΑ ΤΑ ΥΛΙΚΑ ΝΑ ΧΡΗΣΙΜΟΠΟΙΗΘΟΥΝ ΜΕ ΤΗ ΣΥΓΚΑΤΑΘΕΣΗ ΤΟΥ ΑΡΧΙΤΕΚΤΟΝΑ.

2. ΟΛΑ ΤΑ ΑΡΧΙΤΕΚΤΟΝΙΚΑ ΣΧΕΔΙΑ ΚΑΙ ΛΕΠΤΟΜΕΡΕΙΕΣ ΝΑ ΔΙΑΒΑΖΟΝΤΑΙ ΜΑΖΙ ΜΕ ΤΑ ΣΤΑΤΙΚΑ & ΗΛΕΚΤΡΟΜΗΧΑΝΟΛΟΓΙΚΑ ΣΧΕΔΙΑ. ΓΙΑ ΟΠΟΙΕΣΔΗΠΟΤΕ ΔΙΑΦΟΡΕΣ ΝΑ ΕΝΗΜΕΡΩΝΕΤΑΙ Ο ΕΠΙΒΛΕΠΩΝ ΤΟΥ ΕΡΓΟΥ.

3. ΟΙ ΔΙΑΣΤΑΣΕΙΣ ΤΩΝ ΚΟΥΟΝΕΝΟΜΑΤΩΝ ΣΤΑ ΑΡΧΙΤΕΚΤΟΝΙΚΑ ΕΙΝΑΙ ΚΑΘΑΡΕΣ. Ο ΕΡΓΟΛΑΒΟΣ ΕΙΝΑΙ ΥΠΟΧΡΕΟΣ ΝΑ ΚΑΤΑΣΚΕΥΑΣΗ ΤΑ ΚΟΥΟΝΕΝΩΜΑΤΑ ΛΑΜΒΑΝΟΝΤΑΣ ΥΠΟΨΗ 3 ΧΕΡΙΑ ΣΟΥΒΑ ΚΑΙ ΠΟΛΥΣΤΕΡΙΝΗ ΚΑΙ ΟΠΟΙΟΔΗΠΟΤΕ ΤΕΛΙΚΟ ΕΠΙΧΡΙΣΜΑ.

D.W = ΠΛΥΝΤΗΡΙΟ ΠΙΑΤΩΝ
W.M = ΠΛΥΝΤΗΡΙΟ ΡΟΥΧΩΝ
Σ.Ρ = ΣΤΕΓΝΩΤΗΡΙΟ ΡΟΥΧΩΝ
F.. = Φ.ΥΓΕΙΟ
OVEN. = ΟΥΕΝΟΥΡΝΟΣ

BY :	DATE :	REVISION :
-	-	-
-	-	-
-	-	-
-	-	-
-	-	-
-	-	-
-	-	-
-	-	-
-	-	-

EL = EXISTING LEVEL
ΥΦΟΝΙΣΤΑΜΕΝΟ ΥΨ.ΟΜΕΤΡΟ

ERL = EXISTING ROAD LEVEL
ΥΦΟΝΙΣΤΑΜΕΝΟ ΥΨ.ΟΜΕΤΡΟ ΔΡΟΜΟΥ

EPL = EXISTING PAVEMENT LEVEL
ΥΦΟΝΙΣΤΑΜΕΝΟ ΥΨ.ΟΜΕΤΡΟ ΠΕΖΟΔΡΟΜΙΟΥ

PGL = PROPOSED GROUND LEVEL
ΠΡΟΤΕΙΝΟΜΕΝΟ ΥΨ.ΟΜΕΤΡΟ ΕΔΑΦΟΕΝΟΥΣ

FFL = FINISHED FLOOR LEVEL
ΥΨ.ΟΜΕΤΡΟ ΤΕΛΕΙΩΜΕΝΟΥ ΠΑΤΩΜΑΤΟΣ

SSL = STRUCTURAL SLAB LEVEL
ΔΟΜΙΚΟ ΥΨ.ΟΜΕΤΡΟ ΠΛΑΚΑΣ

TOB = TOP OF BEAM
ΔΟΜΙΚΟ ΥΨ.ΟΜΕΤΡΟ ΠΛΑΤΩ ΜΕΡΟΥΣ ΔΟΚΟΥ

TOP = TOP OF PARAPET
ΔΟΜΙΚΟ ΥΨ.ΟΜΕΤΡΟ ΠΛΑΤΩ ΜΕΡΟΥΣ ΣΤΗΘΑΙΟΥ

CODE ARCHITECTURE STUDIO
ARCHITECTS & ENGINEERS

MICHALIS NEOFYTOU
ARCHITECT N.T.U.A.-MA ARCHITECTURE



ΜΙΧΑΛΗΣ ΝΕΟΦΥΤΟΥ
ΑΡΧΙΤΕΚΤΟΝΑΣ
EMP - MA ARCHITECTURE
A.M.: A116407

ΑΓΙΟΥ ΑΝΤΩΝΙΟΥ 6
ΝΙΚΑ ΤOWER FLAT 202
7102, ΑΡΑΔΙΠΠΟΥ
ΛΑΡΝΑΚΑ-ΚΥΠΡΟΣ
TEL. 24534204 FAX. 24323019
EMAIL INFO@CA-STUDIO.COM

JOB TITLE : ΠΟΛΥΚΑΤΟΙΚΙΑ 12 ΔΙΑΜΕΡΙΣΜΑΤΩΝ

OWNER : DEXTEK CONTRACTORS LIMITED

SHEET TITLE : ΟΨΗ Γ

DATE : ΔΕΚΕΜΒΡΙΟΣ 2024

A 10

SCALE : 1 : 100 @ A3

DESIGN

JOB NO

...

594



ΟΨΗ Δ

NOTES :

1. ΟΛΑ ΤΑ ΥΛΙΚΑ ΝΑ ΧΡΗΣΙΜΟΠΟΙΗΘΟΥΝ ΜΕ ΤΗ ΣΥΓΚΑΤΑΘΕΣΗ ΤΟΥ ΑΡΧΙΤΕΚΤΟΝΑ.
2. ΟΛΑ ΤΑ ΑΡΧΙΤΕΚΤΟΝΙΚΑ ΣΧΕΔΙΑ ΚΑΙ ΛΕΠΤΟΜΕΡΕΙΕΣ ΝΑ ΔΙΑΒΑΖΟΝΤΑΙ ΜΑΖΙ ΜΕ ΤΑ ΣΤΑΤΙΚΑ & ΗΛΕΚΤΡΟΜΗΧΑΝΟΛΟΓΙΚΑ ΣΧΕΔΙΑ. ΓΙΑ ΟΠΟΙΕΣΔΗΠΟΤΕ ΔΙΑΦΟΡΕΣ ΝΑ ΕΝΗΜΕΡΩΝΕΤΑΙ Ο ΕΠΙΒΛΕΠΩΝ ΤΟΥ ΕΡΓΟΥ.
3. ΟΙ ΔΙΑΣΤΑΣΕΙΣ ΤΩΝ ΚΟΥΟΝΕΝΟΜΑΤΩΝ ΣΤΑ ΑΡΧΙΤΕΚΤΟΝΙΚΑ ΕΙΝΑΙ ΚΑΘΑΡΕΣ. Ο ΕΡΓΟΛΑΒΟΣ ΕΙΝΑΙ ΥΠΟΧΡΕΩΣ ΝΑ ΚΑΤΑΣΚΕΥΑΣΗ ΤΑ ΚΟΥΟΝΕΝΩΜΑΤΑ ΛΑΜΒΑΝΟΝΤΑΣ ΥΠΟΨΗ 3 ΧΕΡΙΑ ΣΟΥΒΑ ΚΑΙ ΠΟΛΥΣΤΕΡΙΝΗ ΚΑΙ ΟΠΟΙΟΔΗΠΟΤΕ ΤΕΛΙΚΟ ΕΠΙΧΡΙΣΜΑ.
- D.W = ΠΛΥΝΤΗΡΙΟ ΠΙΑΤΩΝ
W.M = ΠΛΥΝΤΗΡΙΟ ΡΟΥΧΩΝ
Σ.Ρ = ΣΤΕΓΝΩΤΗΡΙΟ ΡΟΥΧΩΝ
F.. = Φ.ΥΓΕΙΟ
OVEN. = ΟΥΕΝΟΥΡΝΟΣ

BY :	DATE :	REVISION :
-	-	-
-	-	-
-	-	-
-	-	-
-	-	-
-	-	-
-	-	-
-	-	-
-	-	-

EL = EXISTING LEVEL ΥΦΙΣΤΑΜΕΝΟ ΥΨ.ΟΜΕΤΡΟ	PGL = PROPOSED GROUND LEVEL ΠΡΟΤΕΙΝΟΜΕΝΟ ΥΨ.ΟΜΕΤΡΟ ΕΔΑΦΟΥΣ
ERL = EXISTING ROAD LEVEL ΥΦΙΣΤΑΜΕΝΟ ΥΨ.ΟΜΕΤΡΟ ΔΡΟΜΟΥ	FFL = FINISHED FLOOR LEVEL ΥΨ.ΟΜΕΤΡΟ ΤΕΛΕΙΩΜΕΝΟΥ ΠΛΑΤΩΜΑΤΟΣ
EPL = EXISTING PAVEMENT LEVEL ΥΦΙΣΤΑΜΕΝΟ ΥΨ.ΟΜΕΤΡΟ ΠΕΖΟΔΡΟΜΙΟΥ	SSL = STRUCTURAL SLAB LEVEL ΔΟΜΙΚΟ ΥΨ.ΟΜΕΤΡΟ ΠΛΑΚΑΣ
	TOB = TOP OF BEAM ΔΟΜΙΚΟ ΥΨ.ΟΜΕΤΡΟ ΠΛΑΤΩ ΜΕΡΟΥΣ ΔΟΚΟΥ
	TOP = TOP OF PARAPET ΔΟΜΙΚΟ ΥΨ.ΟΜΕΤΡΟ ΠΛΑΤΩ ΜΕΡΟΥΣ ΣΤΗΘΑΙΟΥ

CODE ARCHITECTURE STUDIO
ARCHITECTS & ENGINEERS

MICHALIS NEOFYTOU
ARCHITECT N.T.U.A.-MA ARCHITECTURE

ΜΙΧΑΛΗΣ ΝΕΟΦΥΤΟΥ
ΑΡΧΙΤΕΚΤΟΝΑΣ
EMP - MA ARCHITECTURE
A.M.: A116407

ΑΓΙΟΥ ΑΝΤΩΝΙΟΥ 6
NIKA TOWER FLAT 202
7102, ARADIPPOY
LARNACA-CYPRUS
TEL. 24534204 FAX. 24323019
EMAIL INFO@CA-STUDIO.COM

JOB TITLE : ΠΟΛΥΚΑΤΟΙΚΙΑ 12 ΔΙΑΜΕΡΙΣΜΑΤΩΝ

OWNER : DEXTEK CONTRACTORS LIMITED

SHEET TITLE : ΟΨΗ Δ

DATE : ΔΕΚΕΜΒΡΙΟΣ 2024

A 1 1


SCALE : 1 : 100 @ A3

DESIGN

T.R

JOB NO

594

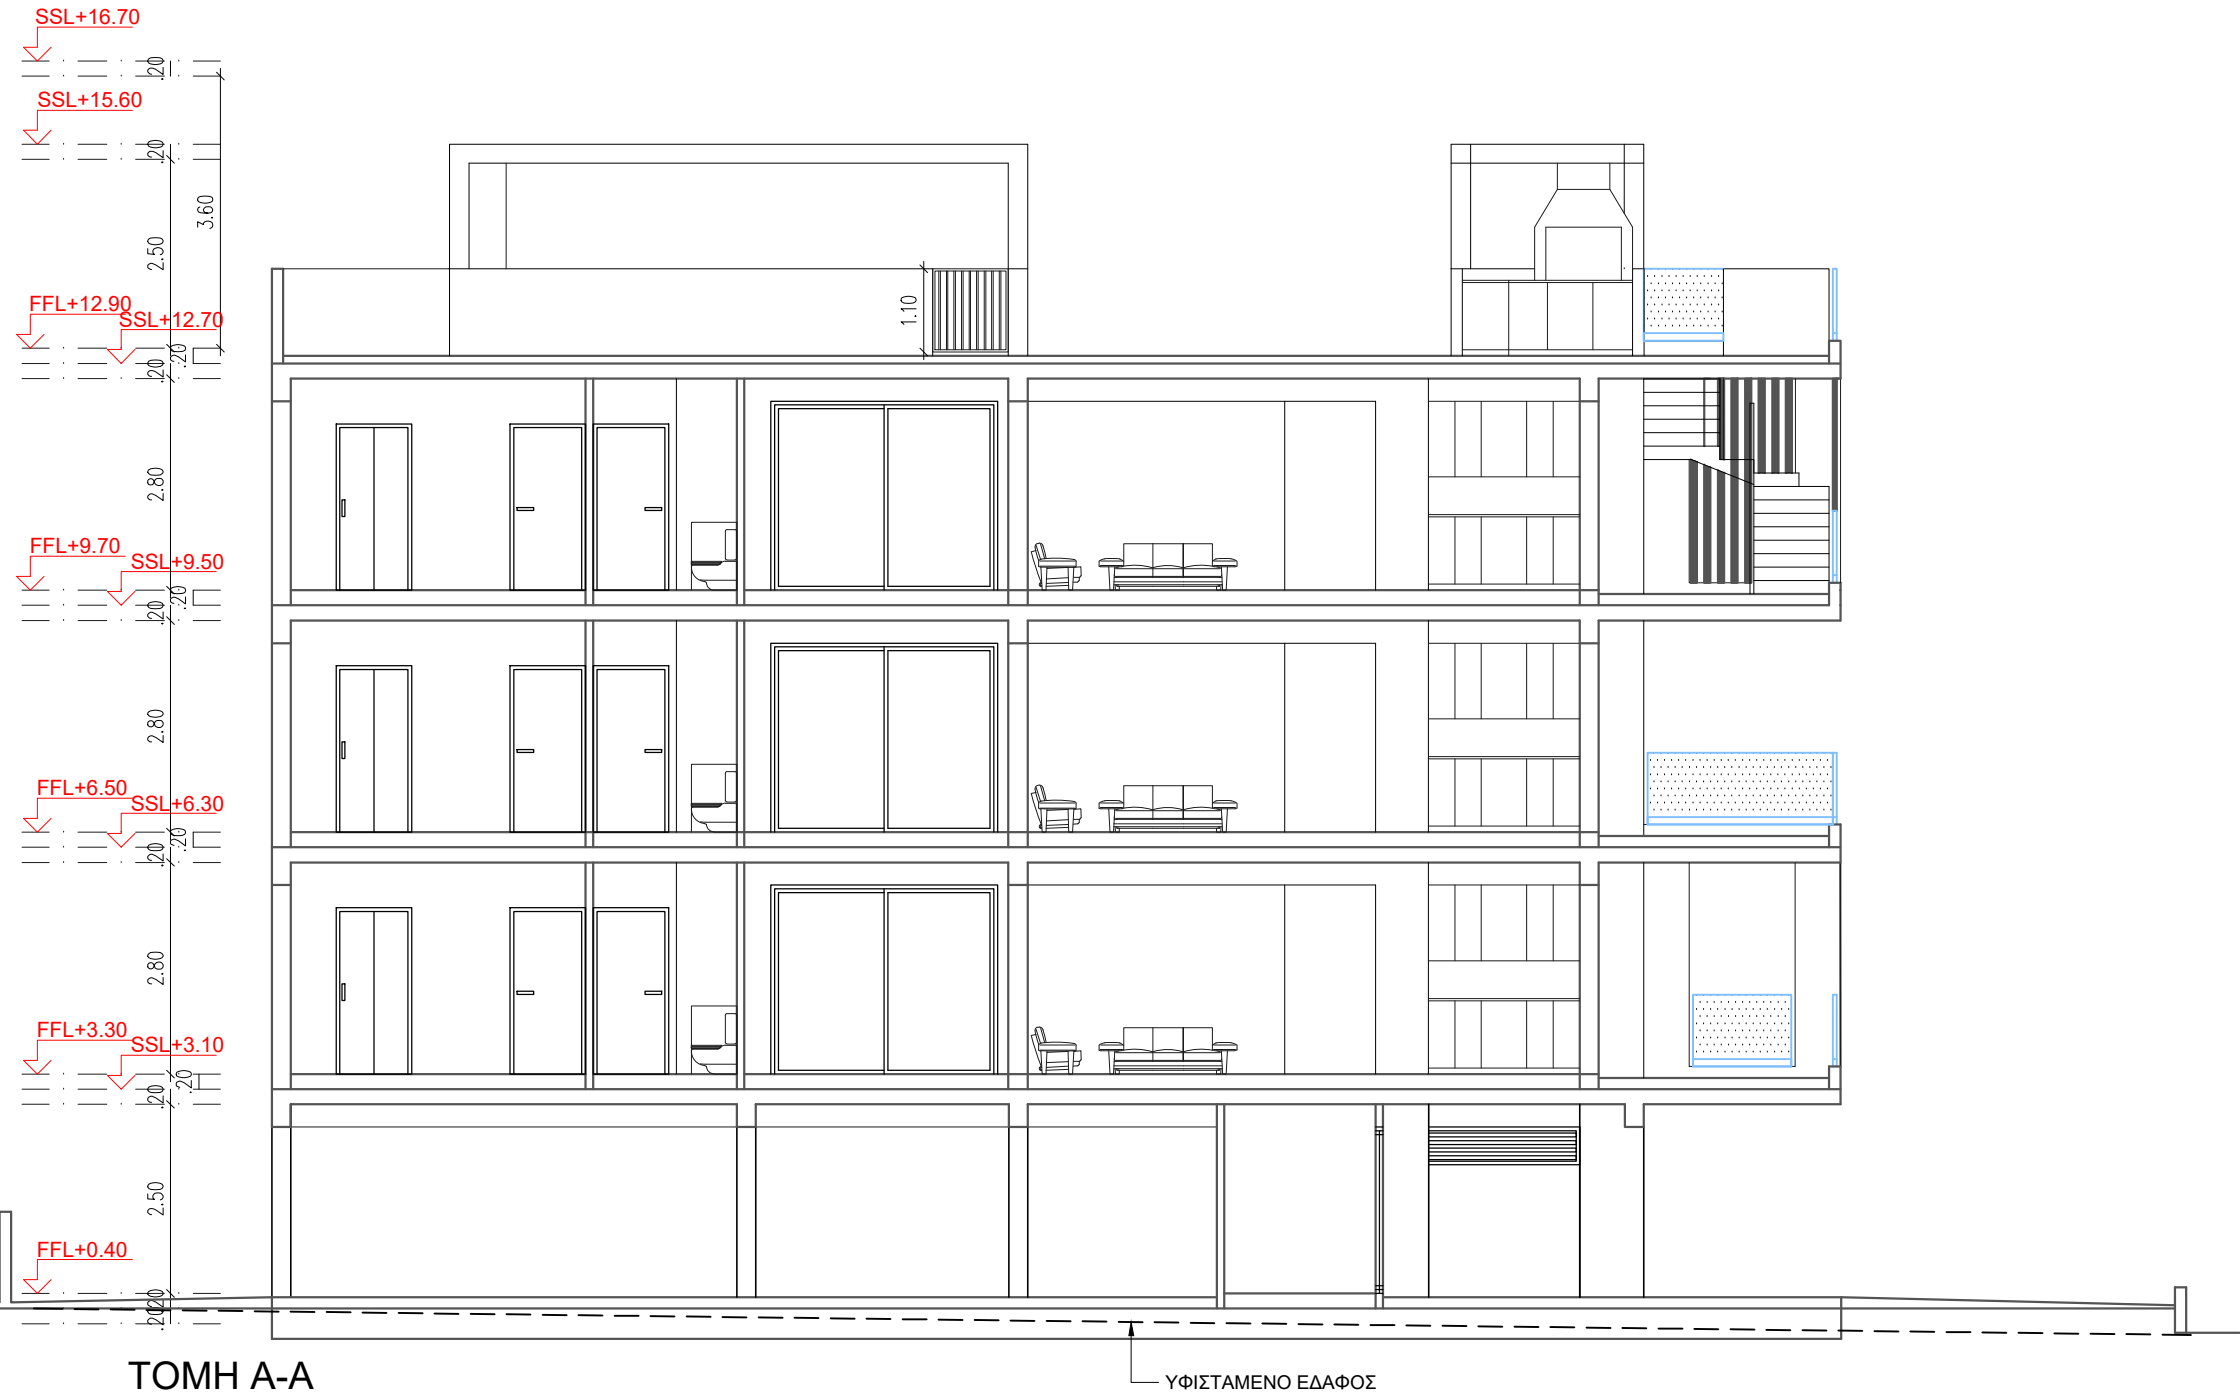

TOMH A-A

ΥΦΙΣΤΑΜΕΝΟ ΕΔΑΦΟΣ

NOTES :		
1. ΟΛΑ ΤΑ ΥΛΙΚΑ ΝΑ ΧΡΗΣΙΜΟΠΟΙΗΘΟΥΝ ΜΕ ΤΗ ΣΥΓΚΑΤΑΘΕΣΗ ΤΟΥ ΑΡΧΙΤΕΚΤΟΝΑ.		
2. ΟΛΑ ΤΑ ΑΡΧΙΤΕΚΤΟΝΙΚΑ ΣΧΕΔΙΑ ΚΑΙ ΛΕΠΤΟΜΕΡΕΙΕΣ ΝΑ ΔΙΑΒΑΖΟΝΤΑΙ ΜΑΖΙ ΜΕ ΤΑ ΣΤΑΤΙΚΑ & ΗΛΕΚΤΡΟΜΗΧΑΝΟΛΟΓΙΚΑ ΣΧΕΔΙΑ. ΓΙΑ ΟΠΟΙΕΣΔΗΠΟΤΕ ΔΙΑΦΕΡΕΣ ΝΑ ΕΝΗΜΕΡΩΝΕΤΑΙ Ο ΕΠΙΒΛΕΠΩΝ ΤΟΥ ΕΡΓΟΥ.		
3. ΟΙ ΔΙΑΣΤΑΣΕΙΣ ΤΩΝ ΚΟΥΟΝΕΝΟΜΑΤΩΝ ΣΤΑ ΑΡΧΙΤΕΚΤΟΝΙΚΑ ΕΙΝΑΙ ΚΑΘΑΡΕΣ. Ο ΕΡΓΟΛΑΒΟΣ ΕΙΝΑΙ ΥΠΟΧΡΕΟΣ ΝΑ ΚΑΤΑΣΚΕΥΑΣΗ ΤΑ ΚΟΥΟΝΕΝΩΜΑΤΑ ΛΑΜΒΑΝΟΝΤΑΣ ΥΠΟΨΗ 3 ΧΕΡΙΑ ΣΟΥΒΑ ΚΑΙ ΠΟΛΥΣΤΕΡΙΝΗ ΚΑΙ ΟΠΟΙΟΔΗΠΟΤΕ ΤΕΛΙΚΟ ΕΠΙΧΡΙΣΜΑ.		
D.W = ΠΛΥΝΤΗΡΙΟ ΠΙΑΤΩΝ W.M = ΠΛΥΝΤΗΡΙΟ ΡΟΥΧΩΝ Σ.Ρ = ΣΤΕΓΝΩΤΗΡΙΟ ΡΟΥΧΩΝ F.. = Φ.ΥΓΕΙΟ OVEN. = ΟΒΕΝΟΥΡΝΟΣ		
BY :	DATE :	REVISION :
-	-	-
-	-	-
-	-	-
-	-	-
-	-	-
-	-	-
-	-	-
-	-	-
-	-	-
-	-	-
EL = EXISTING LEVEL ΥΦΙΣΤΑΜΕΝΟ ΥΨ.ΟΜΕΤΡΟ ERL = EXISTING ROAD LEVEL ΥΦΙΣΤΑΜΕΝΟ ΥΨ.ΟΜΕΤΡΟ ΔΡΟΜΟΥ EPL = EXISTING PAVEMENT LEVEL ΥΦΙΣΤΑΜΕΝΟ ΥΨ.ΟΜΕΤΡΟ ΠΕΖΟΔΡΟΜΙΟΥ PGL = PROPOSED GROUND LEVEL ΠΡΟΤΕΙΝΟΜΕΝΟ ΥΨ.ΟΜΕΤΡΟ ΕΔΑΦΟΥΣ FFL = FINISHED FLOOR LEVEL ΥΨ.ΟΜΕΤΡΟ ΤΕΛΕΙΩΜΕΝΟΥ ΠΙΑΤΩΜΑΤΟΣ SSL = STRUCTURAL SLAB LEVEL ΔΟΜΙΚΟ ΥΨ.ΟΜΕΤΡΟ ΠΛΑΚΑΣ TOB = TOP OF BEAM ΔΟΜΙΚΟ ΥΨ.ΟΜΕΤΡΟ ΠΛΑΤΩ ΜΕΡΟΥΣ ΔΟΚΟΥ TOP = TOP OF PARAPET ΔΟΜΙΚΟ ΥΨ.ΟΜΕΤΡΟ ΠΛΑΤΩ ΜΕΡΟΥΣ ΣΤΗΘΑΙΟΥ		
CODE ARCHITECTURE STUDIO ARCHITECTS & ENGINEERS		
MICHALIS NEOFYTOU ARCHITECT N.T.U.A.-MA ARCHITECTURE  MICHALIS NEOFYTOU ΑΡΧΙΤΕΚΤΟΝΑΣ EMP - MA ARCHITECTURE A.M.: A116407		
ΑΓΙΟΥ ΑΝΤΩΝΙΟΥ 6 NIKA TOWER FLAT 202 7102, ARADIPPOY LARNACA-CYPRUS TEL. 24534204 FAX. 24323019 EMAIL INFO@CA-STUDIO.COM		
JOB TITLE : ΠΟΛΥΚΑΤΟΙΚΙΑ 12 ΔΙΑΜΕΡΙΣΜΑΤΩΝ		
OWNER : DEXTEK CONTRACTORS LIMITED		
SHEET TITLE : ΤΟΜΗ Α-Α		
DATE : ΔΕΚΕΜΒΡΙΟΣ 2024		A 12
SCALE : 1 : 100 @ A3	DESIGN	JOB NO
	T.R	594



TOMH B-B

ΥΦΙΣΤΑΜΕΝΟ ΕΔΑΦΟΣ

NOTES :

- ΟΛΑ ΤΑ ΥΛΙΚΑ ΝΑ ΧΡΗΣΙΜΟΠΟΙΗΘΟΥΝ ΜΕ ΤΗ ΣΥΓΚΑΤΑΘΕΣΗ ΤΟΥ ΑΡΧΙΤΕΚΤΟΝΑ.
 - ΟΛΑ ΤΑ ΑΡΧΙΤΕΚΤΟΝΙΚΑ ΣΧΕΔΙΑ ΚΑΙ ΛΕΠΤΟΜΕΡΕΙΕΣ ΝΑ ΔΙΑΒΑΖΟΝΤΑΙ ΜΑΖΙ ΜΕ ΤΑ ΣΤΑΤΙΚΑ & ΗΛΕΚΤΡΟΜΗΧΑΝΟΛΟΓΙΚΑ ΣΧΕΔΙΑ. ΓΙΑ ΟΠΟΙΕΣΔΗΠΟΤΕ ΔΙΑΦΕΡΟΝΤΕΣ ΝΑ ΕΝΗΜΕΡΩΝΕΤΑΙ Ο ΕΠΙΒΛΕΠΩΝ ΤΟΥ ΕΡΓΟΥ.
 - ΟΙ ΔΙΑΣΤΑΣΕΙΣ ΤΩΝ ΚΟΥΟΥΕΝΟΜΑΤΩΝ ΣΤΑ ΑΡΧΙΤΕΚΤΟΝΙΚΑ ΕΙΝΑΙ ΚΑΘΑΡΕΣ. Ο ΕΡΓΟΛΑΒΟΣ ΕΙΝΑΙ ΥΠΟΧΡΕΟΣ ΝΑ ΚΑΤΑΣΚΕΥΑΣΗ ΤΑ ΚΟΥΟΥΕΝΩΜΑΤΑ ΛΑΜΒΑΝΟΝΤΑΣ ΥΠΟΦ.Η 3 ΧΕΡΙΑ ΣΟΥΒΑ ΚΑΙ ΠΟΛΥΣΤΕΡΙΝΗ ΚΑΙ ΟΠΟΙΟΔΗΠΟΤΕ ΤΕΛΙΚΟ ΕΠΙΧΡΙΣΜΑ.
- D.W = ΠΛΥΝΤΗΡΙΟ ΠΙΑΤΩΝ
W.M = ΠΛΥΝΤΗΡΙΟ ΡΟΥΧΩΝ
Σ.Ρ = ΣΤΕΓΝΩΤΗΡΙΟ ΡΟΥΧΩΝ
F.. = F.ΥΓΕΙΟ
OVEN. = ΟΥΕΝΟΥΡΝΟΣ

BY :	DATE :	REVISION :
-	-	-
-	-	-
-	-	-
-	-	-
-	-	-
-	-	-
-	-	-
-	-	-
-	-	-

EL = EXISTING LEVEL ΥΦΙΣΤΑΜΕΝΟ ΥΦ.ΟΜΕΤΡΟ	PGL = PROPOSED GROUND LEVEL ΠΡΟΤΕΙΝΟΜΕΝΟ ΥΦ.ΟΜΕΤΡΟ ΕΔΑΦΟΥΣ
ERL = EXISTING ROAD LEVEL	FFL = FINISHED FLOOR LEVEL ΥΦ.ΟΜΕΤΡΟ ΤΕΛΕΙΩΜΕΝΟΥ ΠΙΑΤΩΜΑΤΟΣ
EPL = EXISTING PAVEMENT LEVEL	SSL = STRUCTURAL SLAB LEVEL ΔΟΜΙΚΟ ΥΦ.ΟΜΕΤΡΟ ΠΛΑΚΑΣ
ΥΦΙΣΤΑΜΕΝΟ ΥΦ.ΟΜΕΤΡΟ ΠΕΖΟΔΡΟΜΙΟΥ	TOB = TOP OF BEAM ΔΟΜΙΚΟ ΥΦ.ΟΜΕΤΡΟ ΠΛΑΤΩ ΜΕΡΟΥΣ ΔΟΚΟΥ
	TOP = TOP OF PARAPET ΔΟΜΙΚΟ ΥΦ.ΟΜΕΤΡΟ ΠΛΑΤΩ ΜΕΡΟΥΣ ΣΤΗΘΑΙΟΥ

CODE ARCHITECTURE STUDIO
ARCHITECTS & ENGINEERS

MICHALIS NEOFYTOU
ARCHITECT N.T.U.A.-MA ARCHITECTURE

ΜΙΧΑΗΛΗΣ ΝΕΟΦΥΤΟΥ
ΑΡΧΙΤΕΚΤΟΝΑΣ
EMP - MA ARCHITECTURE
A.M.: A116407

ΑΓΙΟΥ ΑΝΤΩΝΙΟΥ 6
ΝΙΚΑ TOWER FLAT 202
7102, ΑΡΑΔΙΠΠΟΥ
LARNACA-CYPRUS
TEL. 24534204 FAX. 24323019
EMAIL INFO@CA-STUDIO.COM

JOB TITLE : ΠΟΛΥΚΑΤΟΙΚΙΑ 12 ΔΙΑΜΕΡΙΣΜΑΤΩΝ

OWNER : DEXTEK CONTRACTORS LIMITED

SHEET TITLE : TOMH B-B

DATE : ΔΕΚΕΜΒΡΙΟΣ 2024

A 13

SCALE : 1 : 100 @ A3

DESIGN
T.R

JOB NO
594